

Design for Feasibility Study
Scope M2 · 3 ทางเลือกผัง · 30.08.2026

คุณทางเข้าเป็นหลัก
พัฒนาจาก OPTION 3 (Meeting 1)

ตัวเลขพื้นที่โดยประมาณ	
พื้นที่อาคาร ชั้น 1 + ชั้น 2	559.6 ตร.ม.
คาตโรปสระ + ทางสัญจร	487.4 ตร.ม.
ผิวน้ำสระ (แข่ง 375.3 + เด็ก 50.0)	425.3 ตร.ม.
หลังคาคลุมสระ 36 x 21 ม.	756.0 ตร.ม.
ที่จอดรถ	24 คัน


ตัวเลขจากการวัดบนแบบ ยังไม่ได้ยืนยันใน AutoCAD ใช้เปรียบเทียบระหว่างทางเลือกเท่านั้น

- **โซนผู้เรียน / นักกีฬา**
ห้องเปลี่ยนเสื้อ อาบน้ำ ล็อกเกอร์
- **โซนผู้ปกครอง / สาธารณะ**
ล็อบบี้ พื้นที่พักผ่อน
- **Mini Café**
เครื่องดื่ม ของว่าง
- **โซนเจ้าหน้าที่ / งานระบบ**
Staff Office ห้องเครื่อง ห้องเคมี
- **พื้นที่ Phase 2**
Fitness Dryland Multipurpose
- **ทางสัญจร / คาเฟ่รอบสระ**
Pool deck ทางเดิน บันได
- **สระแข่งขัน 25 ม. 6 ลู**
375.3 ตร.ม.
- **สระเด็ก 10 x 5 ม. ลึก 0.60**
50.0 ตร.ม.

เทียบกับ 4 แกนเดียวกันทุกทางเลือก

- ### 1. สายตาเจ้าหน้าที่ — จากที่นั่งประจำ มองเห็นอะไร?
- + Staff Office อยู่ปลายซ้ายสุด ติดลานจอดและทางเข้า-ออกคนเข้า-ออกและลานจอดได้ดีที่สุดใน 3 แบบ
 - จากโต๊ะทำงาน มองไม่เห็นสระและพื้นที่คนควรต้องออกมายืนที่อาคารสระเพื่อดูแลผู้เรียน
 - มองไม่เห็นสระเด็กซึ่งอยู่คนละปลายอาคาร
- ### 2. เส้นทางเด็ก — จากระถางถึงขอบสระ ผ่านอะไรบ้าง
- + ห้องอาบน้ำและเปลี่ยนเสื้ออยู่บนแนวทางเดินไปสระพอดี เด็กเปลี่ยนเสื้อเสร็จเดินตรงลงสระได้เลย ไม่ต้องย้อนทาง
 - ที่จอดรถแยก 2 มุ่ง (ด้านซ้ายและด้านหน้า) ยามหรือเจ้าหน้าที่ต้องเดินไปมาระหว่าง 2 จุด
 - ทางเข้าอาคารติดลานจอดโดยตรง ทำเป็น drop-off ไม่ได้ เด็กต้องเดินผ่านแนวช่องจอดรถ
- ### 3. ผู้ปกครอง — นั่งรอรถที่ไหน เห็นลูกหรือไม่
- + พื้นที่พักคอยอยู่ชั้น 2 พร้อม Mini Café มองลงมาเห็นสระจากมุมสูง ไม่รบกวนสมาธิผู้เรียนและผู้สอน
 - อัจฉริยะมีสระ รองรับได้ประมาณ 90 ที่นั่ง
 - ผู้ปกครองที่ต้องดูแลเด็กเล็กใกล้ชิดต้องลงมาชั้น 1
- ### 4. การขยายในอนาคต — ต่อเติมอะไรได้โดยไม่รื้อโครงสร้าง
- + แยกห้องเก็บของออกจากห้องนี้ ทำให้ขยายห้องเครื่องใต้ในอนาคตโดยไม่กระทบพื้นที่อื่น
 - + ชั้น 2 เตรียมโครงสร้างไว้แล้ว เปลี่ยน Multipurpose เป็น Fitness ได้ตาม Phase 2
 - อาคารเป็นแถบยาวชิดขอบที่ดินด้านข้าง การขยาย Lobby ในอนาคตทำได้เฉพาะแนวยาว

A 3D architectural rendering of a modern building complex. The main building features a large, white, gabled roof and a facade with vertical wooden slats. To the left of the main building is a smaller structure with a similar roof, which encloses a swimming pool. A paved walkway leads from the pool area towards the main building. In the foreground, there is a parking lot with several cars parked. The entire complex is surrounded by green grass and some trees, suggesting a landscaped environment.

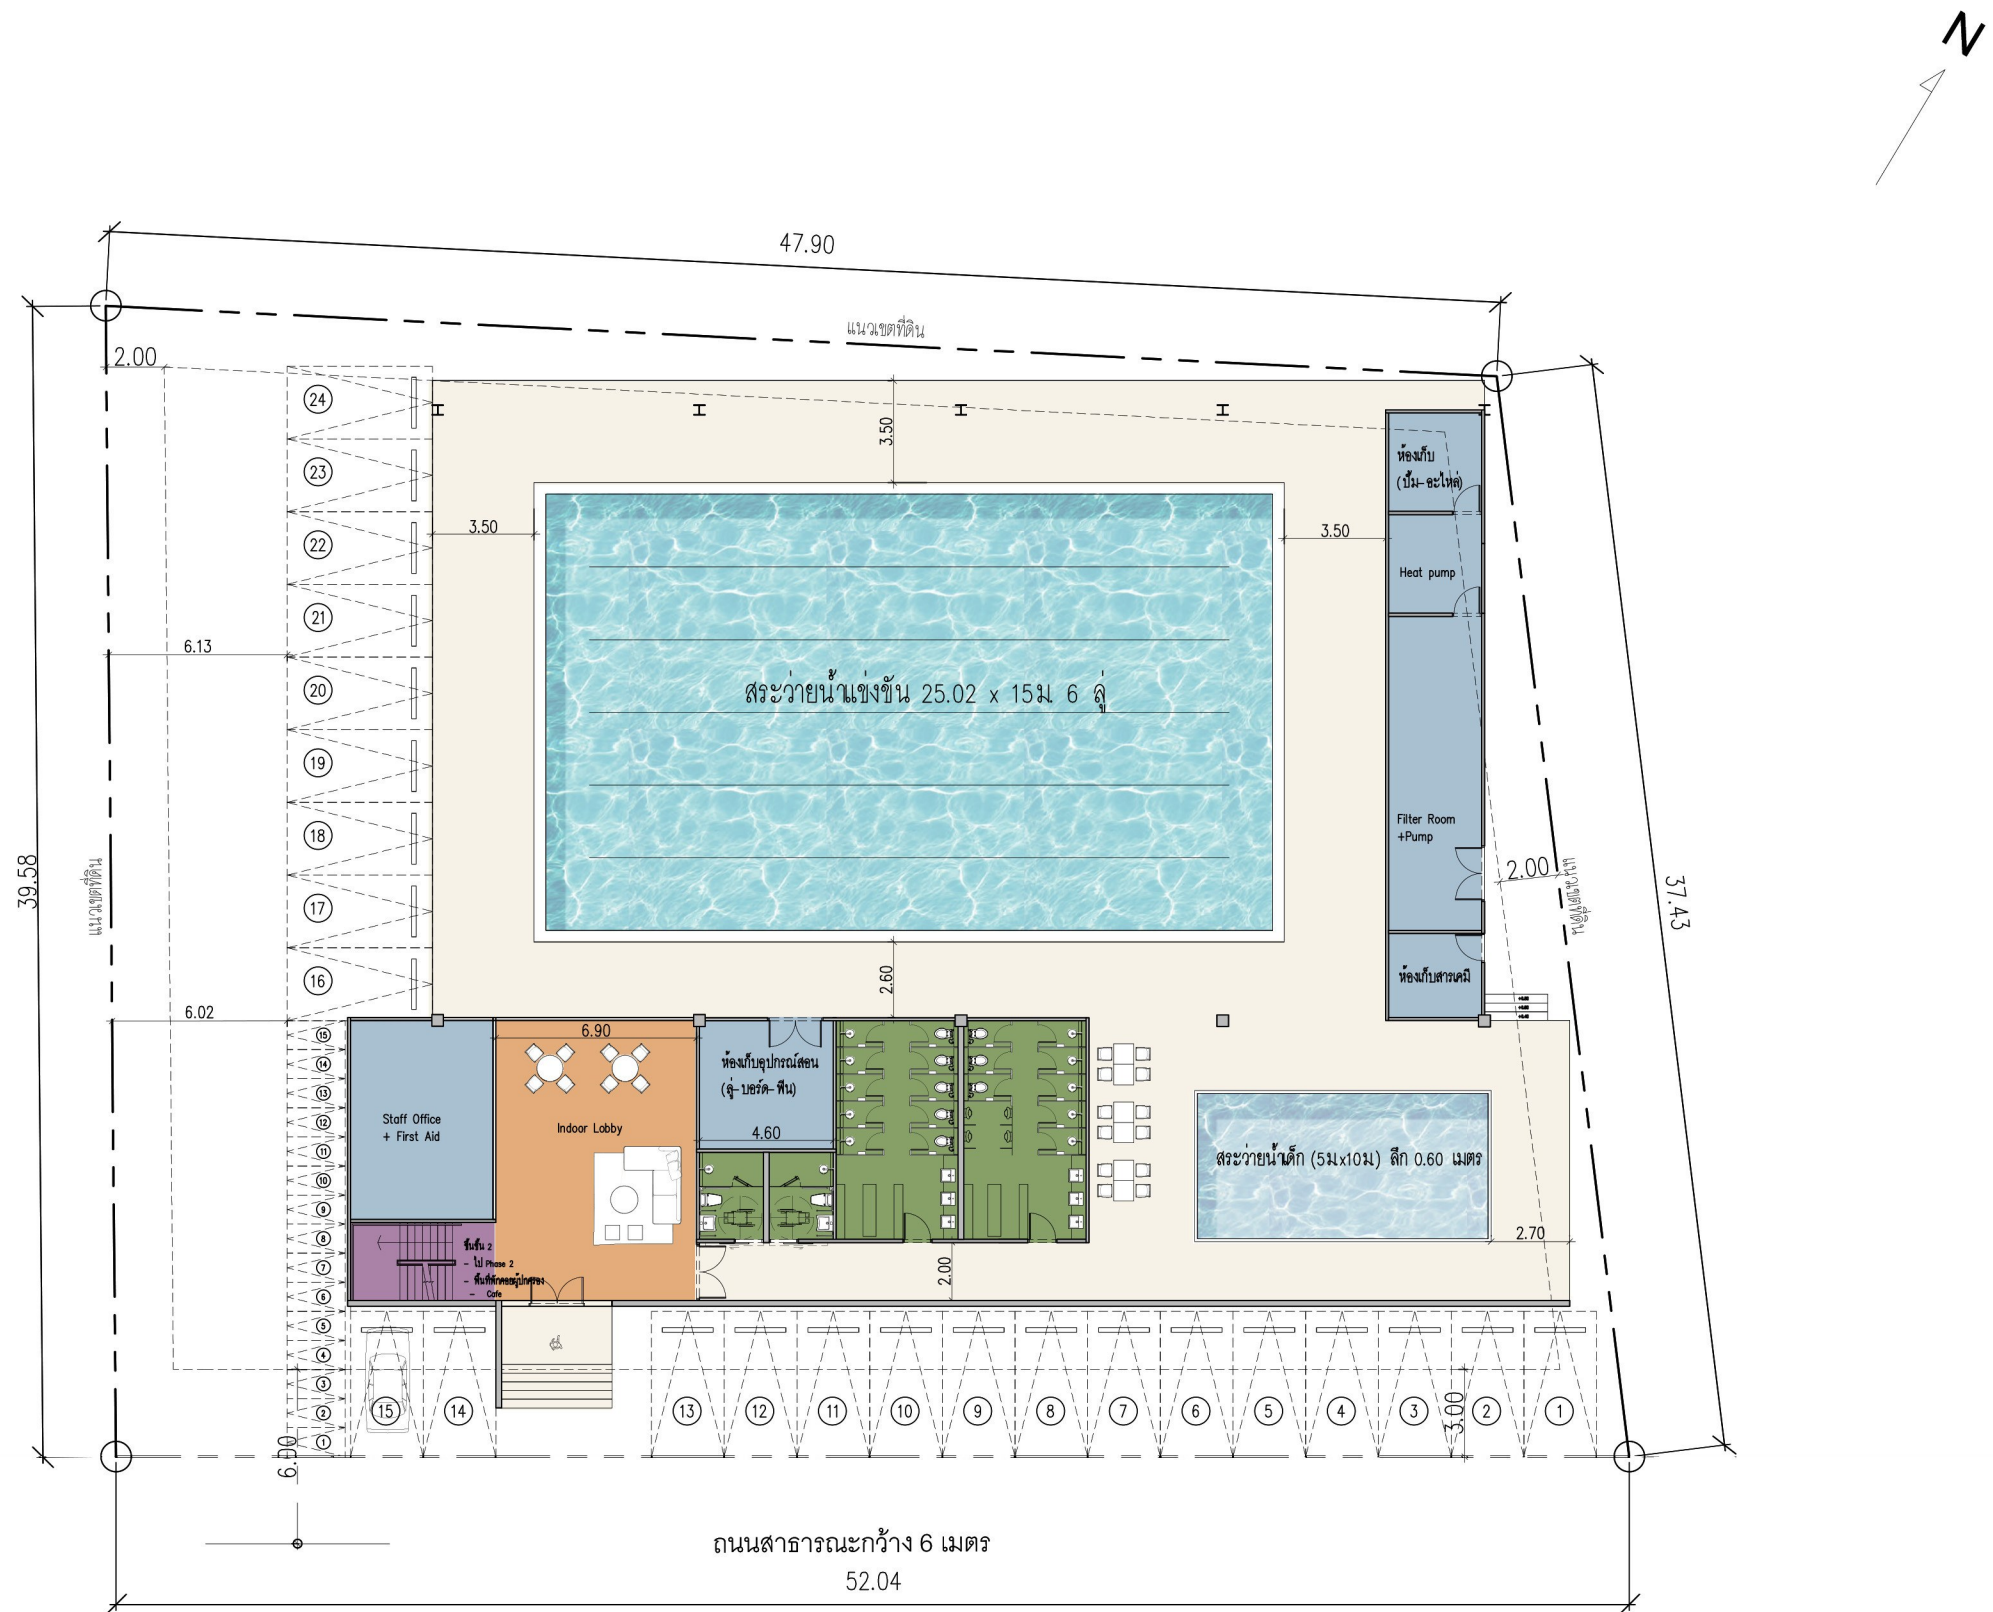

OPTION 1 ชั้น 2

คุมทางเข้าเป็นหลัก
พัฒนาจาก OPTION 3 (Meeting 1)

ตัวเลขพื้นที่โดยประมาณ	
พื้นที่อาคาร ชั้น 1 + ชั้น 2	559.6 ตร.ม.
คาครอบสระ + ทางสัญจร	487.4 ตร.ม.
ผิวน้ำสระ (แข่ง 375.3 + เด็ก 50.0)	425.3 ตร.ม.
หลังคาคลุมสระ 36 × 21 ม.	756.0 ตร.ม.
ที่จอดรถ	24 คัน
ตัวเลขจากการวัดบนแบบ ยังไม่ได้ยืนยันใน AutoCAD ใช้เปรียบเทียบระหว่างทางเลือกเท่านั้น	

- สัญลักษณ์สี
- โซนผู้เรียน / นักกีฬา
ห้องเปลี่ยนเสื้อ อาบน้ำ ล็อกเกอร์
 - โซนผู้ปกครอง / สาธารณะ
ลิโอบบี้ พื้นที่พักผ่อน
 - Mini Café
เครื่องดื่ม ของว่าง
 - โซนเจ้าหน้าที่ / งานระบบ
Staff Office ห้องเครื่อง ห้องเคมี
 - พื้นที่ Phase 2
Fitness Dryland Multipurpose
 - ทางสัญจร / คาครอบสระ
Pool deck ทางเดิน บันได
 - สระแข่งขัน 25 ม. 6 ลู่วิ่ง
375.3 ตร.ม.
 - สระเด็ก 10 × 5 ม. ลึก 0.60 ม.
50.0 ตร.ม.

- ข้อดี / ข้อเสีย ของทางเลือกนี้
- เทียบกับ 4 แคนเดียวกันทุกทางเลือก
- สายคาเจ้าหน้าที่ — จากที่นั่งประจำ มองเห็นอะไร
 - + Staff Office อยู่ปลายซ้ายสุด ติดลานจอดและทางเข้า คุมคนเข้า-ออกและลานจอดได้ดีที่สุดใน 3 แบบ
 - จากโต๊ะทำงาน มองไม่เห็นสระแข่งขัน ครูดึงออกมาในที่คาครอบสระเพื่อดูแลผู้เรียน
 - มองไม่เห็นสระเด็กซึ่งอยู่คนละปลายอาคาร
 - เส้นทางเด็ก — จากระดับถึงขอบสระ ผ่านอะไรบ้าง
 - + ห้องอาบน้ำและเปลี่ยนเสื้ออยู่บนแนวทางเดินไปสระพอดิ เด็กเปลี่ยนเสื้อเสร็จเดินตรงลงสระได้เลย ไม่ต้องย้อนทาง
 - ที่จอดรถแยก 2 ฝั่ง (ด้านซ้ายและด้านหน้า) ยามหรือเจ้าหน้าที่ต้องเดินไปมาระหว่าง 2 จุด
 - ทางเข้าอาคารติดลานจอดโดยตรง ทำเป็น drop-off ไม่ได้ เด็กต้องเดินผ่านแนวช่องจอดรถ
 - ผู้ปกครอง — นั่งรอตรงไหน เห็นลูกหรือไม่
 - + พื้นที่พักผ่อนอยู่ชั้น 2 พร้อม Mini Café มองลงมาเห็นสระจากมุมสูง ไม่รบกวนสมาธิผู้เรียนและผู้สอน
 - + อัฒจรรย์ริมสระ รองรับได้ประมาณ 90 ที่นั่ง
 - ผู้ปกครองที่ต้องดูแลเด็กเล็กใกล้ชิดต้องลงมาชั้น 1
 - การขยายในอนาคต — ต่อเติมอะไรได้โดยไม่รื้อโครงสร้าง
 - + แยกห้องเก็บของออกจากห้องปั๊ม ทำให้ขยายห้องเครื่องได้ในอนาคตโดยไม่กระทบพื้นที่อื่น
 - + ชั้น 2 เตรียมโครงสร้างไว้แล้ว เปลี่ยน Multipurpose เป็น Fitness ได้ตาม Phase 2
 - อาคารเป็นแถบยาวชิดขอบที่ดินด้านล่าง การขยาย Lobby ในอนาคตทำได้เฉพาะแนวยาว

ภาพ 3 มิติ · OPTION 1

