

Design for Feasibility Study
Scope M2 · 3 ทางเลือกผัง · 30.08.2026

พัฒนจาก OPTION 3 (Meeting 1)


ตัวเลขพื้นที่โดยประมาณ	
พื้นที่อาคาร ชั้น 1 + ชั้น 2	568.6 ตร.ม.
คาตโรบสระ + ทางสัญจร	502.6 ตร.ม.
ผิวน้ำสระ (แข่ง 375.3 + เด็ก 50.0)	425.3 ตร.ม.
หลังคาคลุมสระ 36 x 21 ม.	756.0 ตร.ม.
ที่นั่งครด	24 คัน

-  **โซนผู้เรียน / นักกีฬา**
ห้องเปลี่ยนเสื้อ อาบน้ำ สักเกอร์
-  **โซนผู้ปกครอง / สาธารณะ**
ล็อบบี้ พื้นที่พักผ่อน
-  **Mini Café**
เครื่องดื่ม ของว่าง
-  **โซนเจ้าหน้าที่ / งานระบบ**
Staff Office ห้องเครื่อง ห้องเคมี
-  **พื้นที่ Phase 2**
Fitness Dryland Multipurpose
-  **ทางสไลด์ร / คัดครอบสระ**
Pool deck ทางเดิน บันได
-  **สระแข่งขัน 25 ม. 6 ลู**
375.3 ตร.ม.
-  **สระเด็ก 10 x 5 ม. ลึก 0.60**
50.0 ตร.ม.

เทียบกับ 4 แกนเดียวกันทุกทางเลือก

- ### 1. สายตาเจ้าหน้าที่ — จากที่นั่งประจำ มองเห็นอะไร
- + Staff Office ย้ายมาอยู่กลางอาคาร พื้นหน้าเข้าสู่ระบบแข่งขัน
 - ครูเห็นเด็กที่ออกจากห้องเปลี่ยนเสื้อและคนที่อยู่ในสระจากที่นั่งเดียว
 - + แก้วเขียวเรื่องมุมมองของ OPTION 1 โดยตรง ผังส่วนอื่นเหมือนเดิมทุกอย่าง
 - แลมุมตัวอาคารที่ทางเข้าและลานจอดไม่มีคนคุมสายตาโดยตรง
 - ต้องฟังกล้องวงจรปิดหรือจุดยามแยก
- ### 2. เส้นทางเด็ก — จากรถถึงขอบสระ ผ่านอะไรบ้าง
- + ห้องอาบน้ำและเปลี่ยนเสื้ออยู่บนแนวทางเดินไปสระเช่นเดียวกับ OPTION 1
 - + ลีบบั๊กวิ่งขึ้นเป็น 7.15 ม. รั้วผิวใช้ช่วง peak 16.00–20.30 น. ได้ดีกว่า OPTION 1
 - ที่จอดรถแยก 2 ผัง และทางเข้าติดลานจอด ทำ drop-off ไม่ได้ เหมือน OPTION 1
- ### 3. ผู้ปกครอง — นั่งรอรถไหน เห็นลูกหรือไม่
- + พื้นที่พักคอยชั้น 2 พร้อม Mini Café เหมือน OPTION 1
 - + อัฒจันทร์ริมน้ำ รองรับได้ประมาณ 90 ที่นั่ง
 - ผู้ปกครองเด็กเล็กยังต้องลงมาชั้น 1 เหมือนเดิม
- ### 4. การขายในอนาคด — ต่อเติมอะไรได้โดยไม่รื้อโครงสร้าง
- + ย้ายห้องเก็บอุปกรณ์สอนไปปลายชาย ทำให้แกนกลางอาคารเป็นโซนควบคุมปรับ function ในอนาคดได้ง่ายกว่า
 - + ห้องเครื่องขยายได้เหมือน OPTION 1
 - ผังอาคารเหมือน OPTION 1 การขายในอนาคดจึงมีข้อจำกัดเดียวกัน

A 3D architectural rendering of a modern building complex. The main building features a large, white, gabled roof and a facade with vertical wooden slats. Adjacent to the building is a swimming pool with a blue interior. A paved parking lot with yellow markings is situated in front of the building, with several cars parked. The entire complex is surrounded by green lawns and various trees, including palm trees. A grey concrete wall runs along the bottom edge of the scene.

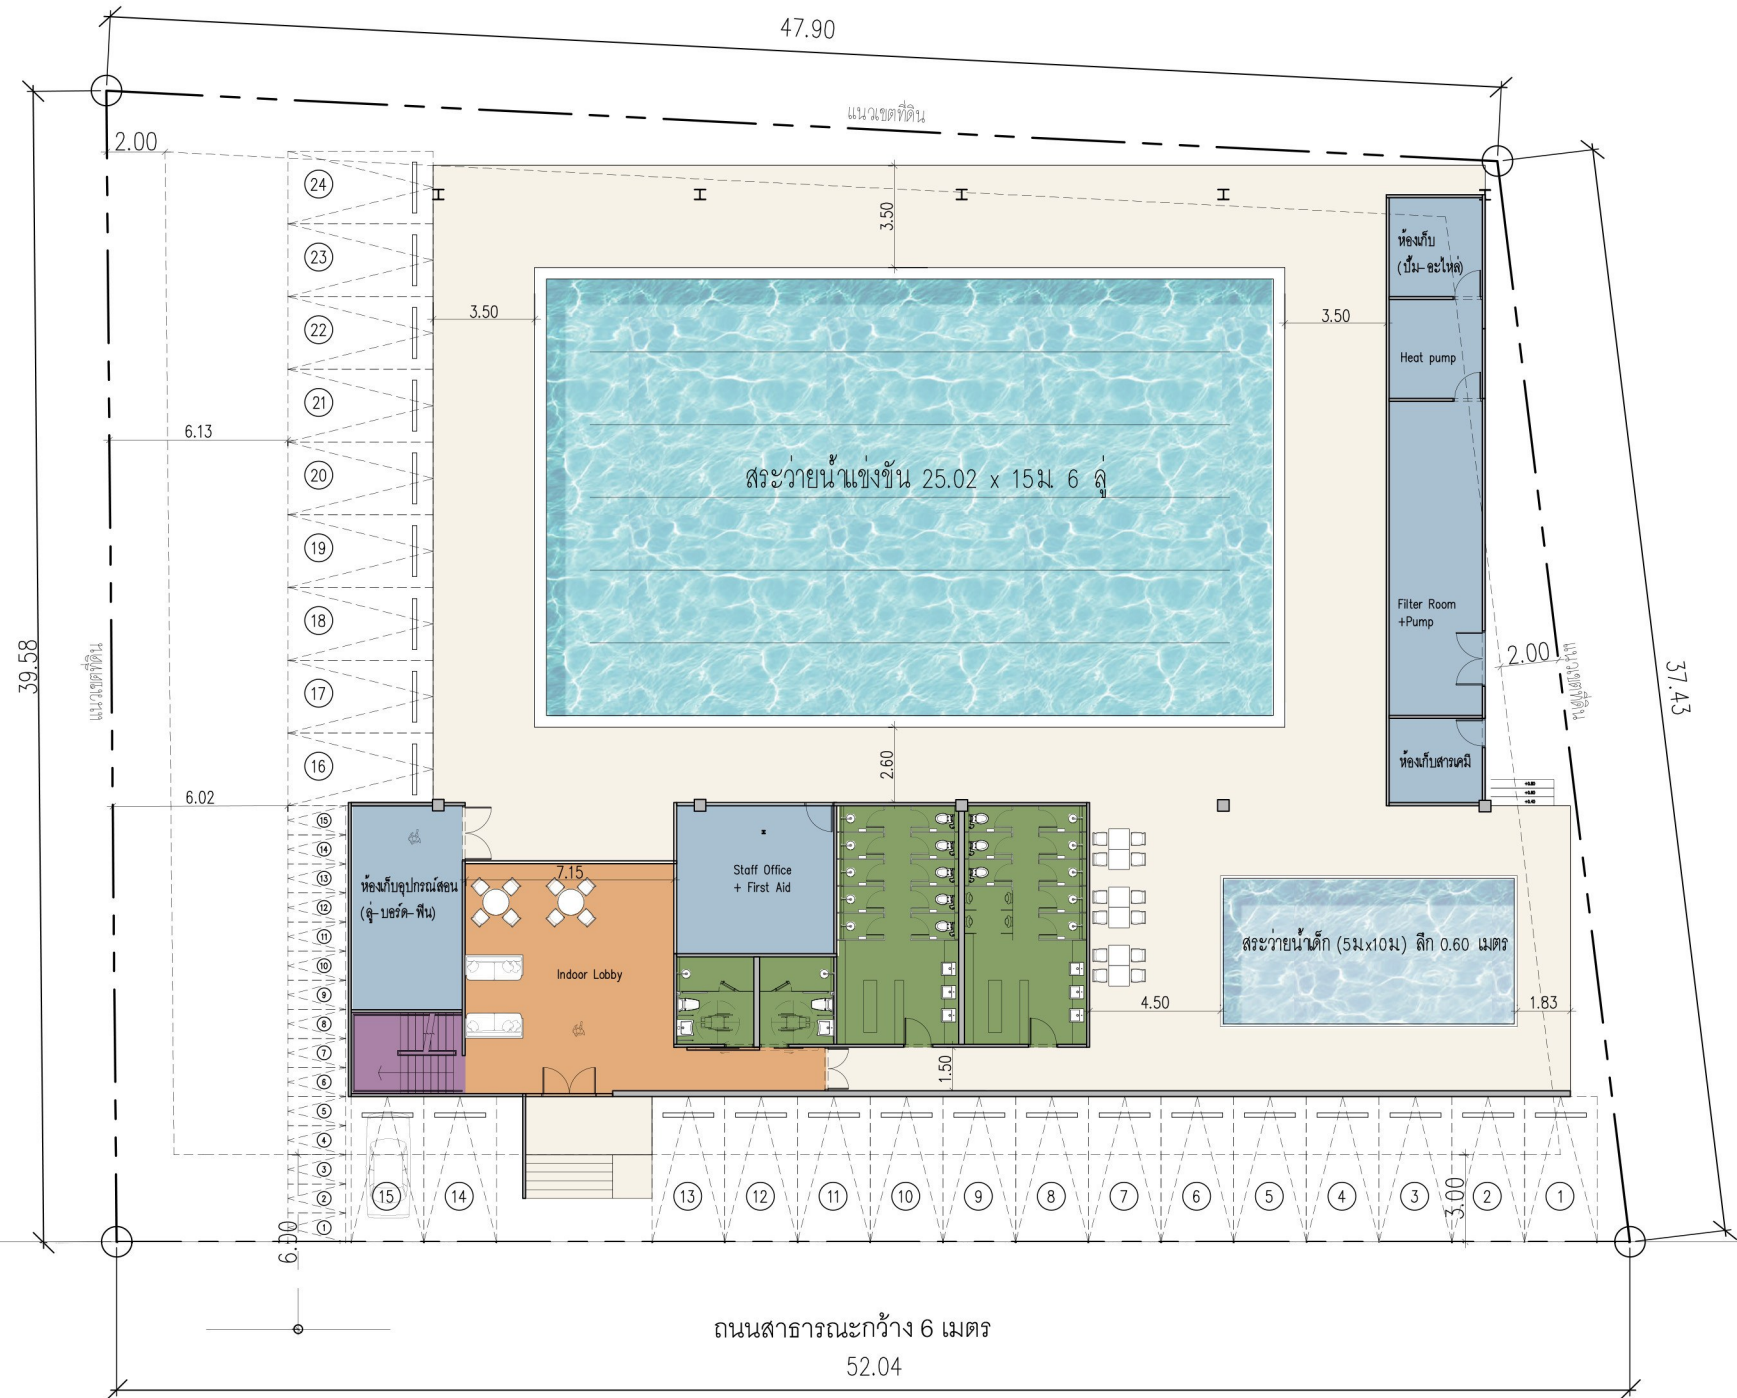

OPTION 2 ^{ชั้น 2}

คุ่มสระเป็นหลัก
พัฒนาจาก OPTION 3 (Meeting 1)

ตัวเลขพื้นที่โดยประมาณ	
พื้นที่อาคาร ชั้น 1 + ชั้น 2	568.6 ตร.ม.
คาครอบสระ + ทางสัญจร	502.6 ตร.ม.
ผิวน้ำสระ (แข่ง 375.3 + เด็ก 50.0)	425.3 ตร.ม.
หลังคาคลุมสระ 36 × 21 ม.	756.0 ตร.ม.
ที่จอดรถ	24 คัน
ตัวเลขจากการวัดบนแบบ ยังไม่ได้ยืนยันใน AutoCAD ใช้เปรียบเทียบระหว่างทางเลือกเท่านั้น	

- สัญลักษณ์สี
- โซนผู้เรียน/ นักกีฬา
ห้องเปลี่ยนเสื้อ อาบน้ำ ล็อกเกอร์
 - โซนผู้ปกครอง/ สาธารณะ
ลิโอบบี้ พื้นที่พักผ่อน
 - Mini Café
เครื่องดื่ม ของว่าง
 - โซนเจ้าหน้าที่/ งานระบบ
Staff Office ห้องเครื่อง ห้องเคมี
 - พื้นที่ Phase 2
Fitness Dryland Multipurpose
 - ทางสัญจร/ คาครอบสระ
Pool deck ทางเดิน บันได
 - สระแข่งขัน 25 ม. 6 ลู่
375.3 ตร.ม.
 - สระเด็ก 10 × 5 ม. ลึก 0.60 ม.
50.0 ตร.ม.

- ข้อดี/ ข้อเสีย ของทางเลือกนี้
- เทียบกับ 4 แคนเดียวกันทุกทางเลือก
- สายคาเจ้าหน้าที่ — จากที่นี้ประจำ มองเห็นอะไร
 - + Staff Office ย้ายมาอยู่กลางอาคาร พื้นหน้าเข้าสู่สระแข่งขัน
ครูเห็นทั้งเด็กที่ออกจากห้องเปลี่ยนเสื้อและคนที่อยู่ในสระจากที่นี้คนเดียว
 - + แก้ข้อเสียเรื่องมุมมองของ OPTION 1 โดยตรง ฝั่งส่วนอื่นเหมือนเดิมทุกอย่าง
 - แลกมาด้วยการที่ทางเข้าและลานจอดไม่มีคนคุมสายตาโดยตรง
ต้องพึ่งกล้องวงจรปิดหรือจุดยามแยก
 - เส้นทางเด็ก — จากระดับถึงขอบสระ ผ่านอะไรบ้าง
 - + ห้องอาบน้ำและเปลี่ยนเสื้ออยู่บนแนวทางเดินไปสระเช่นเดียวกับ OPTION 1
 - + ลิโอบบี้กว้างขึ้นเป็น 7.15 ม. รับผู้ใช้ช่วง peak 16.00–20.30 น. ได้ดีกว่า OPTION 1
 - ที่จอดรถแยก 2 ฝั่ง และทางเข้าติดลานจอด ทำ drop-off ไม่ได้ เหมือน OPTION 1
 - ผู้ปกครอง — นั่งรอตรงไหน เห็นลูกหรือไม่
 - + พื้นที่พักผ่อนชั้น 2 พร้อม Mini Café เหมือน OPTION 1
 - + อัฒจันทร์ริมสระ รองรับได้ประมาณ 90 ที่นั่ง
 - ผู้ปกครองเด็กเล็กยังต้องลงมาชั้น 1 เหมือนเดิม
 - การขายในอนาคด — ต่อเติมอะไรได้โดยไม่รื้อโครงสร้าง
 - + ย้ายห้องเก็บอุปกรณ์สอนไปปลายซ้าย ทำให้แกนกลางอาคารเป็นโซนควบคุม
ปรับ function ในอนาคดได้ง่ายกว่า
 - + ห้องเครื่องขยายได้เหมือน OPTION 1
 - ฝั่งอาคารเหมือน OPTION 1 การขยายในอนาคตจึงมีข้อจำกัดเดียวกัน

ภาพ 3 มิติ · OPTION 2

