

OPTION 3 ชั้น 1


คุ่มทั้งสองสระ + one-way
พัฒนาจาก OPTION 4 (Meeting 1)

ตัวเลขพื้นที่โดยประมาณ	
พื้นที่อาคาร ชั้น 1 + ชั้น 2	538.7 ตร.ม.
คาครอบสระ + ทางสัญจร	532.7 ตร.ม.
ผิวน้ำสระ (แข่ง 375.3 + เด็ก 50.0)	425.3 ตร.ม.
หลังคาคลุมสระ 36 x 21 ม.	756.0 ตร.ม.
ที่จอดรถ	24 คัน
ตัวเลขจากการวัดบนแบบ ยังไม่ได้ยืนยันใน AutoCAD ใช้เปรียบเทียบระหว่างทางเลือกเท่านั้น	

- สัญลักษณ์สี
- โซนผู้เรียน / นักกีฬา
ห้องเปลี่ยนเสื้อ อาบน้ำ ล็อกเกอร์
 - โซนผู้ปกครอง / สาธารณะ
ลิโอบบี้ พื้นที่พักผ่อน
 - Mini Café
เครื่องดื่ม ของว่าง
 - โซนเจ้าหน้าที่ / งานระบบ
Staff Office ห้องเครื่อง ห้องเคมี
 - พื้นที่ Phase 2
Fitness Dryland Multipurpose
 - ทางสัญจร / คาครอบสระ
Pool deck ทางเดิน บันได
 - สระแข่งขัน 25 ม. 6 ลู่
375.3 ตร.ม.
 - สระเด็ก 10 x 5 ม. ลึก 0.60 ม.
50.0 ตร.ม.

- ข้อดี / ข้อเสีย ของทางเลือกนี้
- เทียบกับ 4 แคนเดียวกันทุกทางเลือก
- สายตาเจ้าหน้าที่ — จากที่นั่งประจำ มองเห็นอะไร
+ Staff Office เห็นทั้งสระแข่งขันและสระเด็กพร้อมกันจากจุดเดียว
ครอบคลุมที่สุดใน 3 แบบ
+ สระทั้งสองอยู่ในโซนสายตาเดียวกัน ลดจำนวนเจ้าหน้าที่ที่ต้องประจำจุด
- ห้อง Staff Office เล็กกว่า OPTION 1 และ 2 ต้องตรวจสอบว่าพอสำหรับทีมงาน 4-5 คนพร้อมที่เก็บเอกสาร
 - เส้นทางเด็ก — จากระถางขอบสระ ผ่านอะไรบ้าง
+ ที่จอดรถรวมเป็นแถบเดียวด้านหน้า เดินรถ one-way ได้จริง คุ่มจุดเดียว
+ มีพื้นที่ drop-off จอดเทียบต่อเนื่องหลายคัน
เด็กเดินเข้าอาคารได้โดยไม่ต้องตัดผ่านแนวช่องจอด
ตรงกับความสะดวกหลักของเจ้าของโครงการ
- ทางเข้าห้องน้ำเชื่อมทับกับพื้นที่สระเด็ก
คนเดินไปห้องน้ำกับเด็กที่กำลังเรียนใช้ทางเดียวกัน ต้องแก้ไขในขั้น Design Development
 - ผู้ปกครอง — นั่งรอตรงไหน เห็นลูกหรือไม่
+ อัจฉริยะ 4 ชั้น รองรับได้ประมาณ 120 ที่นั่ง มากที่สุดใน 3 แบบ
+ ชั้น 2 เป็นแถวยาวขนานสระ มองเห็นสระจากด้านข้างตลอดแนว
+ วันแข่งขัน เปลี่ยนพื้นที่ Indoor Dryland เป็นพื้นที่ชมการแข่งขันเพิ่มเติม
 - การขายยาในอนาคต — ต่อเติมอะไรได้โดยไม่รื้อโครงสร้าง
+ พื้นที่ห้องเครื่องและงานระบบสระใหญ่ที่สุด
รองรับการเพิ่มอุปกรณ์และการซ่อมบำรุงระยะยาวได้ดีที่สุด
+ สระเด็กอยู่ชิดอาคารและโซนห้องเปลี่ยนเสื้อ ผู้ปกครองเดินถึงได้เร็วที่สุด
+ ชั้น 2 มีพื้นที่โล่งมาก กันห้องเพิ่มได้ภายหลังเมื่อรู้ความต้องการจริง
โดยไม่ต้องรื้อโครงสร้างหลัก

ภาพ 3 มิติ · OPTION 3

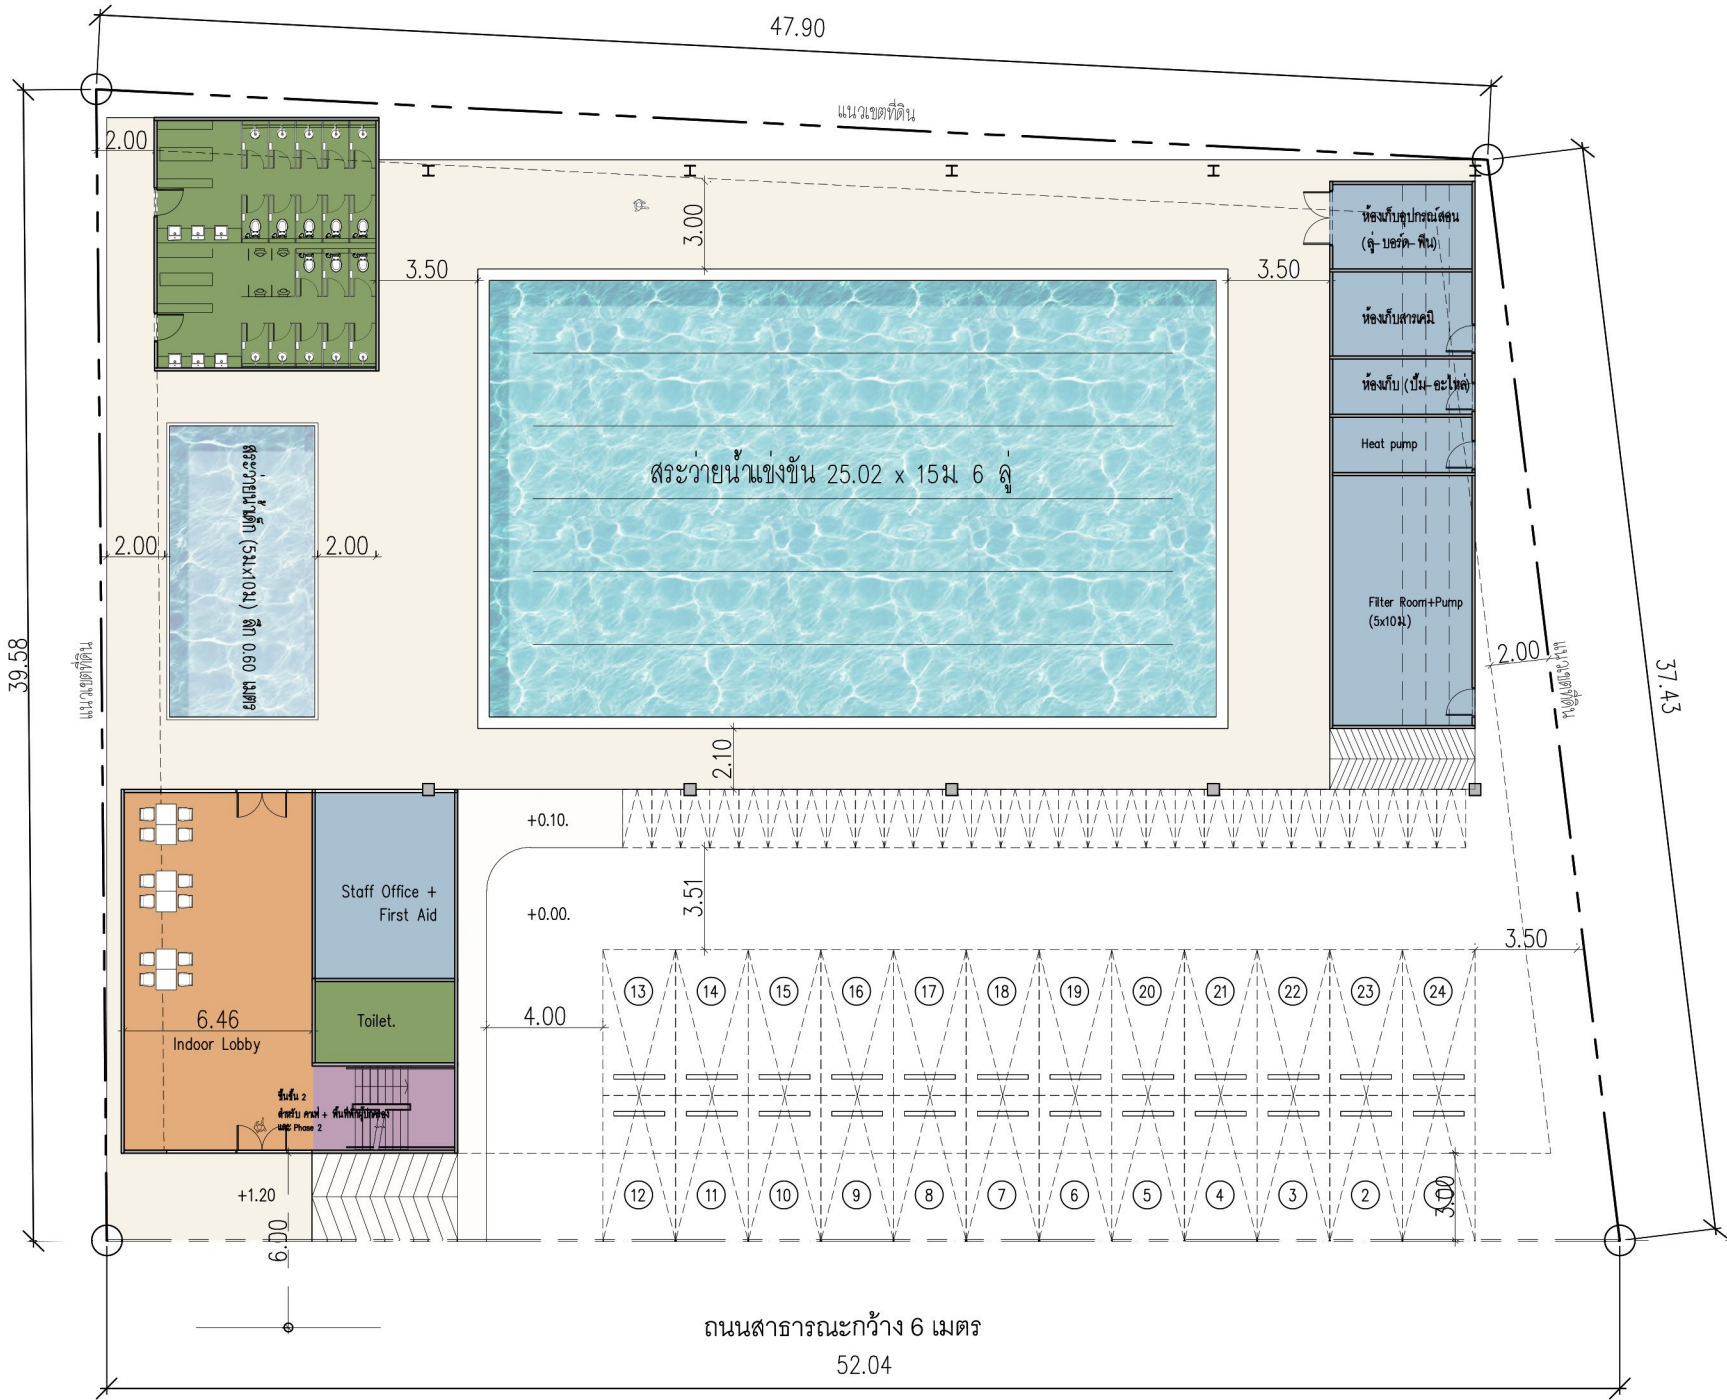

OPTION 3

ชั้น 2

คุ่มทั้งสองสระ + one-way

พัฒนาจาก OPTION 4 (Meeting 1)

ตัวเลขพื้นที่โดยประมาณ	
พื้นที่อาคาร ชั้น 1 + ชั้น 2	538.7 ตร.ม.
คาครอบสระ + ทางสัญจร	532.7 ตร.ม.
ผิวน้ำสระ (แข่ง 375.3 + เด็ก 50.0)	425.3 ตร.ม.
หลังคาคลุมสระ 36 × 21 ม.	756.0 ตร.ม.
ที่จอดรถ	24 คัน
ตัวเลขจากการวัดบนแบบ ยังไม่ได้ยืนยันใน AutoCAD ใช้เปรียบเทียบระหว่างทางเลือกเท่านั้น	

- สัญลักษณ์สี
- โซนผู้เรียน / นักกีฬา

ห้องเปลี่ยนเสื้อ อาบน้ำ ล็อกเกอร์

โซนผู้ปกครอง / สาธารณะ

ลิโอบบี้ พื้นที่พักผ่อน

Mini Café

เครื่องดื่ม ของว่าง

โซนเจ้าหน้าที่ / งานระบบ

Staff Office ห้องเครื่อง ห้องเคมี

พื้นที่ Phase 2

Fitness Dryland Multipurpose

ทางสัญจร / คาครอบสระ

Pool deck ทางเดิน บันได

สระแข่งขัน 25 ม. 6 ลู่

375.3 ตร.ม.

สระเด็ก 10 × 5 ม. ลึก 0.60 ม.

50.0 ตร.ม.

- ข้อดี / ข้อเสีย ของทางเลือกนี้
- เทียบกับ 4 แคนเดียวกันทุกทางเลือก
1. สายตาเจ้าหน้าที่ — จากที่นั่งประจำ มองเห็นอะไร

+ Staff Office เห็นทั้งสระแข่งขันและสระเด็กพร้อมกันจากจุดเดียว

+ ครอบคลุมที่สุดใน 3 แบบ

+ สระทั้งสองอยู่ในโซนสายตาเดียวกัน ลดจำนวนเจ้าหน้าที่ที่ต้องประจำจุด

- ห้อง Staff Office เล็กกว่า OPTION 1 และ 2 ต้องตรวจสอบว่าพอสำหรับทีมงาน 4-5 คนพร้อมที่เก็บเอกสาร
2. เส้นทางเด็ก — จากระถางถึงขอบสระ ผ่านอะไรบ้าง

+ ที่จอดรถรวมเป็นแถบเดียวด้านหน้า เดินรถ one-way ได้จริง คุ่มจุดเดียว

+ มีพื้นที่ drop-off จอดเทียบต่อเนื่องหลายคัน

+ เด็กเดินเข้าอาคารได้โดยไม่ต้องตัดผ่านแนวช่องจอด

+ ตรงกับความกังวลหลักของเจ้าของโครงการ

- ทางเข้าห้องน้ำเชื่อมทับกับพื้นที่สระเด็ก

+ คนเดินไปห้องน้ำกับเด็กที่กำลังเรียนใช้ทางเดียวกัน ต้องแก้ไขในขั้น Design Development
3. ผู้ปกครอง — นั่งรอตรงไหน เห็นลูกหรือไม่

+ อัฒจรรย์ 4 ชั้น รองรับได้ประมาณ 120 ที่นั่ง มากที่สุดใน 3 แบบ

+ ชั้น 2 เป็นแถวยาวขนานสระ มองเห็นสระจากด้านข้างตลอดแนว

+ วันแข่งขัน เปลี่ยนพื้นที่ Indoor Dryland เป็นพื้นที่ชมการแข่งขันเพิ่มเติม
4. การขยายในอนาคต — ต่อเติมอะไรได้โดยไม่รื้อโครงสร้าง

+ พื้นที่ห้องเครื่องและงานระบบสระใหญ่ที่สุด

+ รองรับการเพิ่มอุปกรณ์และการซ่อมบำรุงระยะยาวได้ดีที่สุด

+ สระเด็กอยู่ชิดอาคารและโซนห้องเปลี่ยนเสื้อ ผู้ปกครองเดินถึงได้เร็วที่สุด

+ ชั้น 2 มีพื้นที่โล่งมาก กันห้องเพิ่มได้ภายหลังเมื่อรู้ความต้องการจริง

+ โดยไม่ต้องรื้อโครงสร้างหลัก

ภาพ 3 มิติ · OPTION 3

