

M3 ^{ั้}ชั้น 1

พัฒนาจาก OPTION 3 (Meeting 2)

ตามความเห็นที่ลงนาม 4 กันยายน 2569

ตัวเลขพื้นที่โดยประมาณ

พื้นที่อาคาร ชั้น 1 + ชั้น 2	552.5 ตร.ม.
คาบรอบสระ + ทางสัญจร	534.2 ตร.ม.
ผิวน้ำสระ (แข่ง 375.3 + เด็ก 50.0)	425.3 ตร.ม.
หลังคาคลุมสระ 36 x 21 ม.	756.0 ตร.ม.
อัฒจันทร์ 4 แถว บนหลังห้องเครื่อง	93.4 ตร.ม.
ที่จอดรถ	24 คัน


ตัวเลขจากการวัดบนแบบ ยังไม่ได้ยืนยันใน AutoCAD
ใช้เทียบเคียงระดับ Feasibility เท่านั้น

สัญลักษณ์หน้าสี

- โซนผู้เรียน / นักกีฬา
ห้องเปลี่ยนเสื้อ อาบน้ำ ล็อกเกอร์
- โซนผู้ปกครอง / สาธารณะ
ลิโอบบี้ พื้นที่พักผ่อน
- Mini Café
เครื่องดื่ม ของว่าง
- โซนเจ้าหน้าที่ / งานระบบ
Staff Office ห้องเครื่อง ห้องเคมี
- พื้นที่ Fitness · Dryland · Multipurpose
เตรียมโครงสร้างรองรับ Phase 2
- ทางสัญจร / คาบรอบสระ
Pool deck ทางเดิน บันได
- สระแข่งขัน 25 ม. 6 คู
375.3 ตร.ม.
- สระเด็ก 10 x 5 ม. ลึก 0.60 ม.
50.0 ตร.ม.

ชั้น 1 คงเดิมจาก M2 ทั้งหมด

- สระแข่งขัน 25.02 x 15 ม. 6 คู ระบบ Overflow และสระเด็ก 10 x 5 ม. ลึก 0.60 ม.
- Staff Office + First Aid เห็นทั้งสองสระจากจุดเดียว
- ทางเข้า-ออกแบบ one-way จุด drop-off เด็กไม่ต้องตัดผ่านลานจอดรถ
- ห้องเครื่อง ห้องสารเคมี Heat pump และ Filter Room รวมอยู่แถบทิศตะวันออก
- ลานจอดรถ 24 คัน ผิวน้ำซึมผ่านได้
- ห้องเปลี่ยนเสื้อ / ล็อกเกอร์ 64.1 ตร.ม. อยู่ระหว่างทางเข้ากับขอบสระ

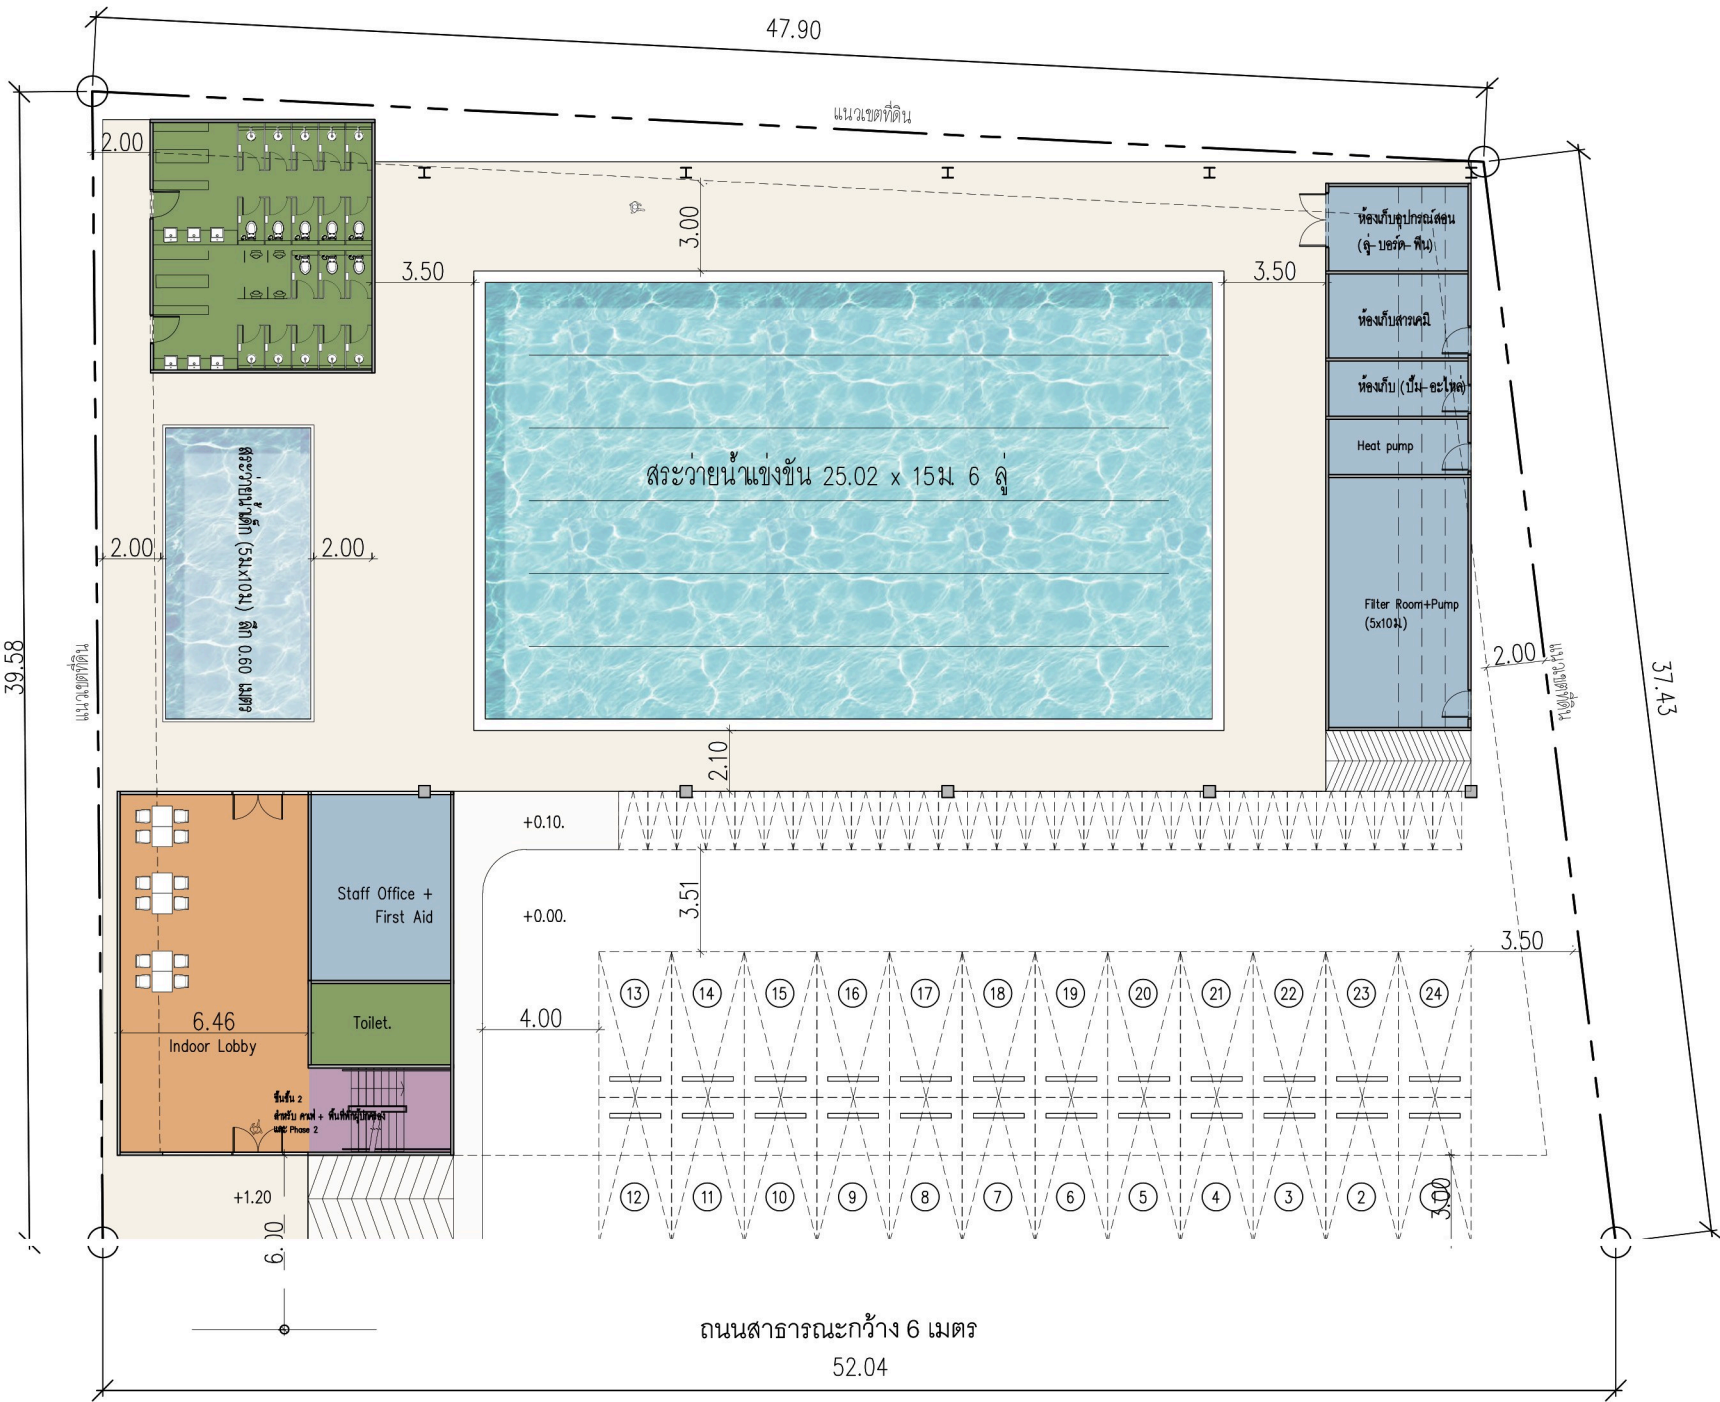

พัฒนาจาก OPTION 3 (Meeting 2)

ตัวเลขพื้นที่โดยประมาณ

พื้นที่อาคาร ชั้น 1 + ชั้น 2	552.5 ตร.ม.
คาบรถบัสระ + ทางสัญจร	534.2 ตร.ม.
ผิวน้ำสระ (แบ่ง 375.3 + เด็ก 50.0)	425.3 ตร.ม.
หลังคาคลุมสระ 36 × 21 ม.	756.0 ตร.ม.
อัฒจันทร์ 4 แถว บนหลังห้องเครื่อง	93.4 ตร.ม.
ที่จอดรถ	24 คัน

ตัวเลขจากการวัดบนแบบ ยังไม่ได้ยืนยันใน AutoCAD
ใช้เทียบเคียงระดับ Feasibility เท่านั้น

■ **โซนผู้เรียน/ นักกีฬา**
ห้องเปลี่ยนเสื้อ อาบน้ำ ล็อกเกอร์

■ **โซนผู้ปกครอง / สาธารณะ**
 ล็อบบี้ พื้นที่พักผ่อน

Mini Café
เครื่องดื่ม ของว่าง

■ **โซนเจ้าหน้าที่ / งานระบบ**
Staff Office ห้องเครื่อง ห้องเคมี

พื้นที่ Fitness · Dryland · Multipurpose
เตรียมโครงสร้างรองรับ Phase 2

■ ทางสัญจร / ดาดรอบสระ
Pool deck ทางเดิน บันได

■ **สระแข่งขัน 25 ม. 6 คู่**
375.3 ตร.ม.

■ สระเด็ก 10 x 5 ม. ลึก 0.60 ม.
50.0 ตร.ม.

- พื้นที่ที่จอดรถผู้ปกครอง 93.5 ตร.ม. รวม Mini Café อยู่ด้านทิศเหนือ มองเห็นสระได้
- Multipurpose 50.8 · Indoor Dryland 51.1 · Indoor Fitness 57.4 ตร.ม. เรียงเป็นแถวเดียว
- ทุกห้องเข้าจากทางเดินฝั่งสระกว้าง 3.00 ม. ไม่ต้องเดินผ่านโซนผู้ปกครอง
- Multipurpose และ Dryland ใช้บันไดขึ้นเปิดเป็นพื้นที่ชมการแข่งขันได้
- กระจกห้อง Fitness และ Dryland เป็นกระจกทึบ เพื่อความเป็นส่วนตัวและสมาธิของผู้ฝึก
- ห้องน้ำ 2 ห้อง ห้องเก็บของ และบันได อยู่มุมทิศใต้ ตำแหน่งเดิม
- อัฒจันทร์ 4 แถว ประมาณ 120 ที่นั่ง อยู่เหนือแถบห้องเครื่องฝั่งทิศตะวันออก

