

OPTION 3



ARCHE AQUATICS
Design for Feasibility Study
MEETING 1 — 6 LAYOUTS

Gross Floor Area (GFA) =

- ข้อดี ADVANTAGES
- โถงต้อนรับใหญ่ เห็นวิวสระ
 - Amphitheater ฝั่งตั้งฉากกับลู่วิ่ง
 - โซนพักผ่อนอยู่ชั้น 2 แยกผปก - นักเรียนชัดเจน
 - จุดปล่อยตัว หัวสระ ระยะ 4.3 เมตร

- ข้อเสีย DISADVANTAGES
- ห้องเครื่องนระบบ ห้องเก็บของทั้งหมดของสระ
น้อยลง 33% ให้ที่จอดรถ + Pool deck
 - เช่น Filter + Pump room ตั้งไว้ 50 ตร.ม (5x10). เหลือ 32 ตร.ม(8x4)
 - สระเด็กเล็ก เด็กโต deck ต่อกัน
 - หัวสระ (จุดปล่อยตัวระยะไม่ถึง 3.5 เมตร)

3D MASSING

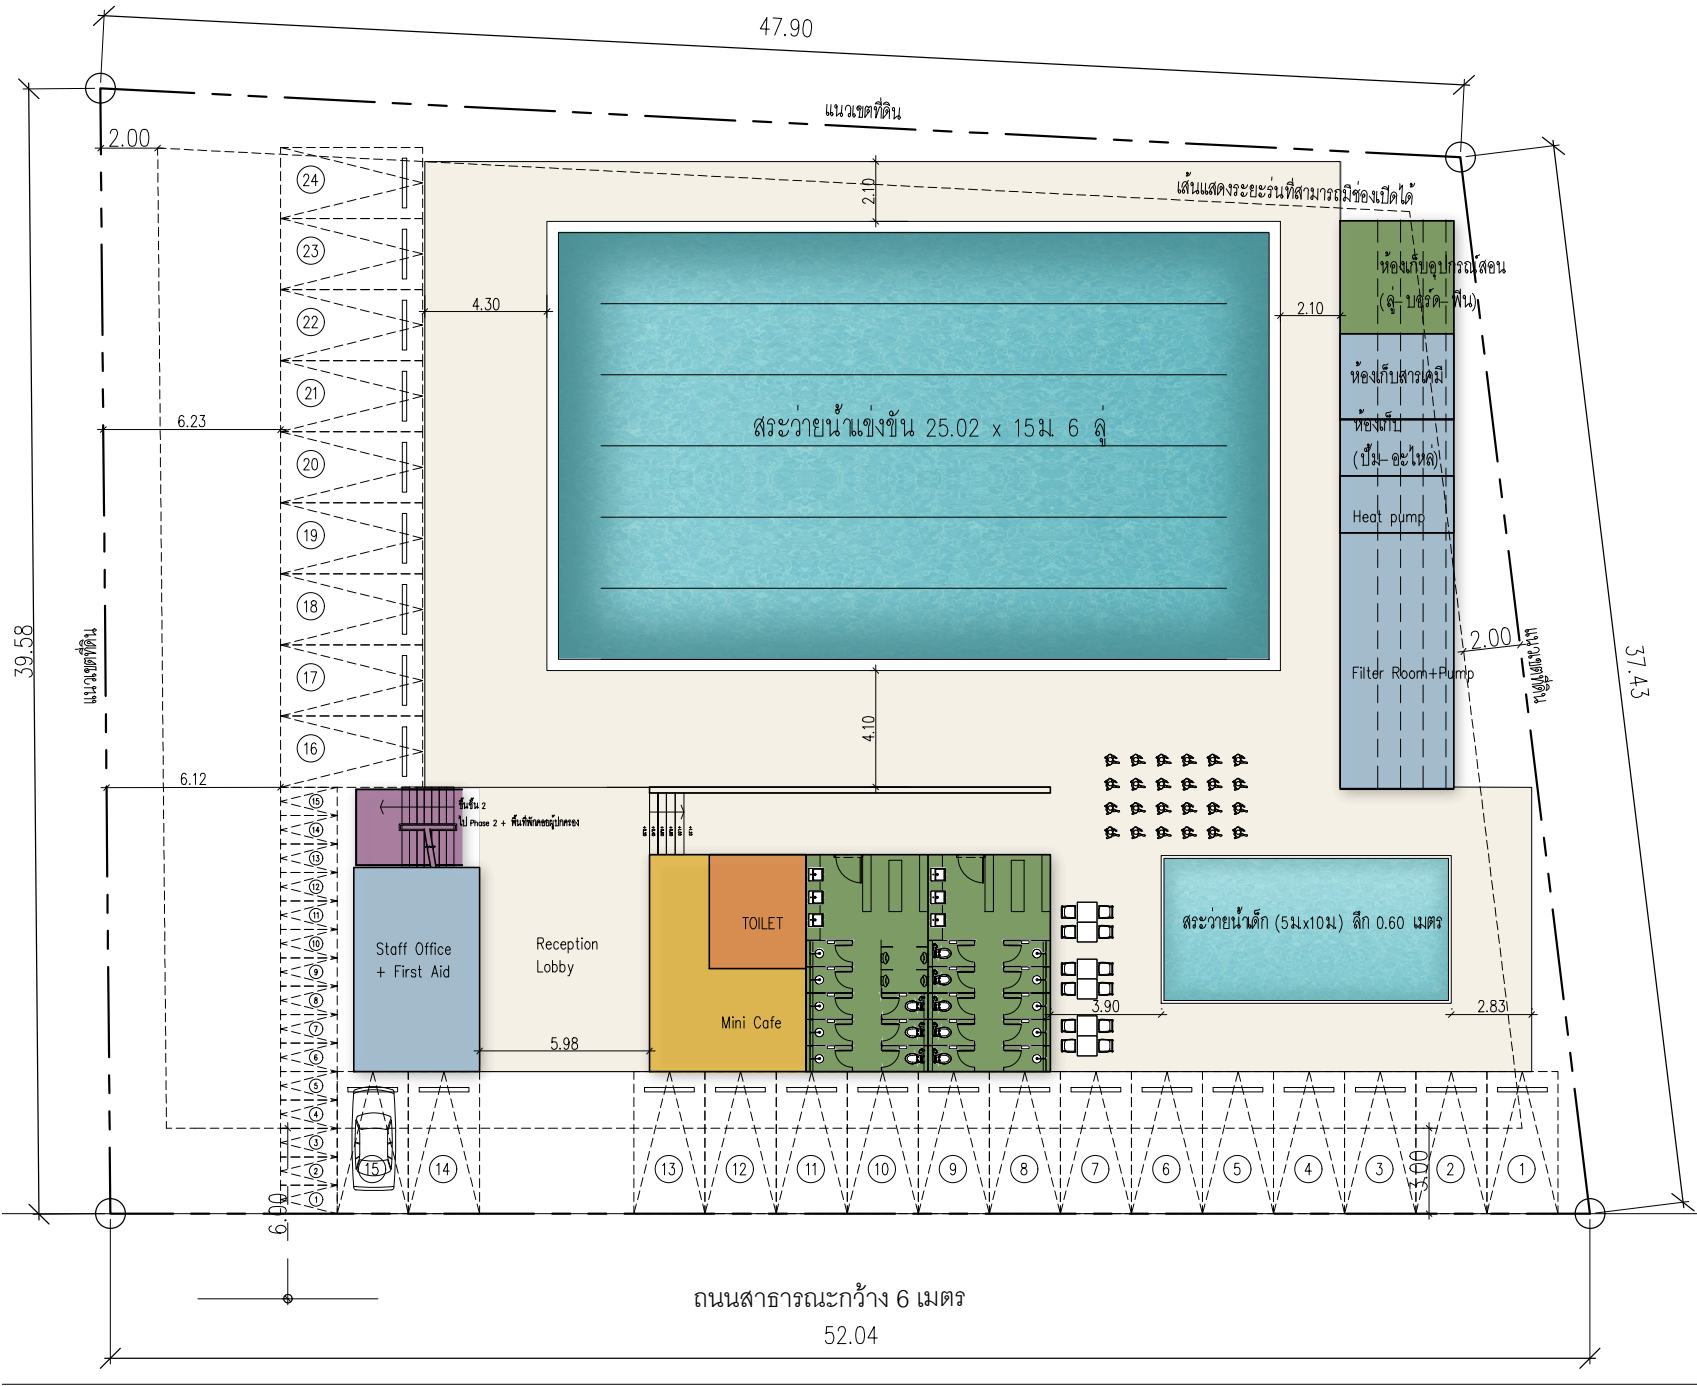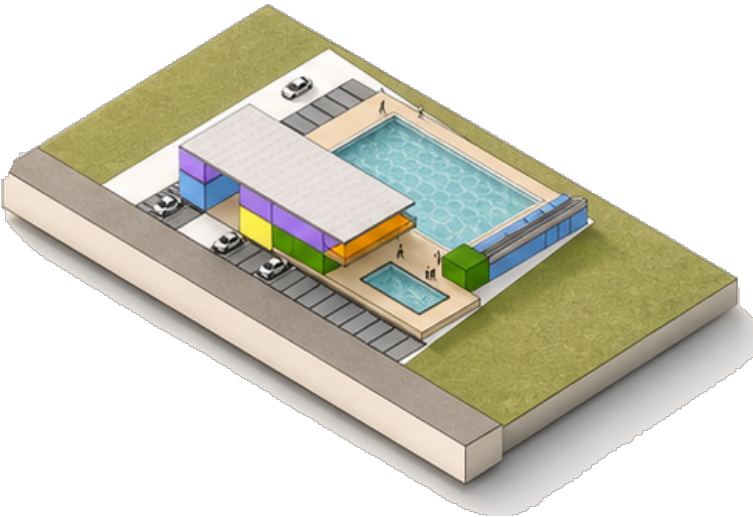

LEGEND / ZONING

- โซนการใช้งาน / ZONING
- ส่วนนักกีฬาว่ายน้ำ Swimmer / athlete zone
 - ส่วนผู้ปกครอง / สาธารณะ Parent / public zone
 - คาเฟ่ Mini Café
 - ส่วนเจ้าหน้าที่ / งานระบบ Staff-only access — office, first aid, MEP
 - Phase 2 ชั้น 2 : คาเฟ่ + พื้นที่ผู้ปกครอง

- พื้นที่สัญจร / CIRCULATION
- พื้นสระ / ลานรอบสระ / โถงต้อนรับ Pool deck, lobby, entrance steps — one tone

- สระว่ายน้ำ / WATER
- สระแข่งขัน 25 x 15 ม. ลึก 1.20 – 1.60 ม. สไลด์ (ลิ้น = ด้านลึก)
 - สระเด็ก 5 x 10 ม. ลึก 0.60 ม. Learner pool

สีทึบ = ห้อง (มีผนัง) สีครีม = พื้นที่สัญจรและลานเปิดโล่งทั้งหมด
Solid tone = enclosed room Cream = all deck / circulation