

Design for Feasibility Study  
Scope M2 · 3 ทางเลือกผัง · 30.08.2026

## คุมทางเข้าเป็นหลัก

พัฒนาจาก OPTION 3 (Meeting 1)


|                                    |             |
|------------------------------------|-------------|
| พื้นที่อาคาร ชั้น 1 + ชั้น 2       | 559.6 ตร.ม. |
| คาบรอบสระ + ทางสัญจร               | 487.4 ตร.ม. |
| ผิวน้ำสระ (แข่ง 375.3 + เด็ก 50.0) | 425.3 ตร.ม. |
| หลังคาคลุมสระ 36 × 21 ม.           | 756.0 ตร.ม. |
| ที่จอดรถ                           | 24 คัน      |

ตัวเลขจากการวัดบนแบบ ยังไม่ได้ยืนยันใน AutoCAD ใช้เปรียบเทียบระหว่างทางเลือกเท่านั้น

- **โซนผู้เรียน / นักกีฬา**  
ห้องเปลี่ยนเสื้อ อาบน้ำ ล็อกเกอร์
- **โซนผู้ปกครอง / สาธารณะ**  
ล็อบบี้ พื้นที่พักผ่อน
- **Mini Café**  
เครื่องดื่ม ของว่าง
- **โซนเจ้าหน้าที่ / งานระบบ**  
Staff Office ห้องเครื่อง ห้องเคมี
- **พื้นที่ Phase 2**  
Fitness Dryland Multipurpose
- **ทางสัญจร / คาคอบบะ**  
Pool deck ทางเดิน บันได
- **สระแข่งขัน 25 ม. 6 ลู**  
375.3 ตร.ม.
- **สระเด็ก 10 x 5 ม. ลึก 0.60**  
50.0 ตร.ม.

เทียบกับ 4 แกนเดียวกันทุกทางเลือก

- ### 1. สายตาเจ้าหน้าที่ — จากที่นั่งประจำ มองเห็นอะไร
- + Staff Office อยู่ปลายซ้ายสุด ติดลานจอดรถและทางเข้า
  - คมคนเข้า-ออกและลานจอดได้ดีที่สุดใน 3 แบบ
  - จากโต๊ะทำงาน มองไม่เห็นสระแข่งขัน
  - ครูต้องออกมายืนที่อาคารสระเพื่อดูผู้เรียน
  - มองไม่เห็นสระเด็กซึ่งอยู่คนละปลายอาคาร
- ### 2. เส้นทางเด็ก — จากรถถึงขอบสระ ผ่านอะไรบ้าง
- + ห้องอาบน้ำและเปลี่ยนเสื้ออยู่บนแนวทางเดินไปสระพอดี
  - เด็กเปลี่ยนเสื้อเสร็จเดินตรงลงสระได้เลย ไม่ต้องย้อนทาง
  - ที่จอดรถแยก 2ฝั่ง (ด้านซ้ายและด้านหน้า)
  - ยามหรือเจ้าหน้าที่ต้องเดินไปมาระหว่าง 2 จุด
  - ทางเข้าอาคารติดลานจอดโดยตรง ทำเป็น drop-off ไม่ได้
  - เด็กต้องเดินผ่านแนวช่องจอดรถ
- ### 3. ผู้ปกครอง — นั่งรถรอไหน เห็นลูกหรือไม่
- + พื้นที่ที่กักคอย่ออยู่ 2 พร้อม Mini Café มองลงมาเห็นสระจากมุมสูง
  - ไม่รบกวนสมาธิผู้เรียนและผู้สอน
  - + อัดวงจรยืมสระ รองรับได้ประมาณ 90 ที่นั่ง
  - ผู้ปกครองที่ต้องดูแลเด็กเล็กใกล้ขีดต้องลงมาชั้น 1
- ### 4. การขายยาในอาคาร — ต่อเติมอะไรได้โดยไม่รื้อโครงสร้าง
- + แยกห้องเก็บของออกจากห้องบ่ม
  - ทำให้ขายของเครื่องได้ในอนาคตโดยไม่กระทบพื้นที่อื่น
  - + ชั้น 2 เตรียมโครงสร้างไว้แล้ว เปลี่ยน Multipurpose เป็น Fitness ได้ตาม Phase 2
  - สระเด็กอยู่มุมขวา ไม่มีเงาอาคารบัง โดนแดดบ่ายเต็ม ต้องเผื่องบกันแดดเพิ่ม

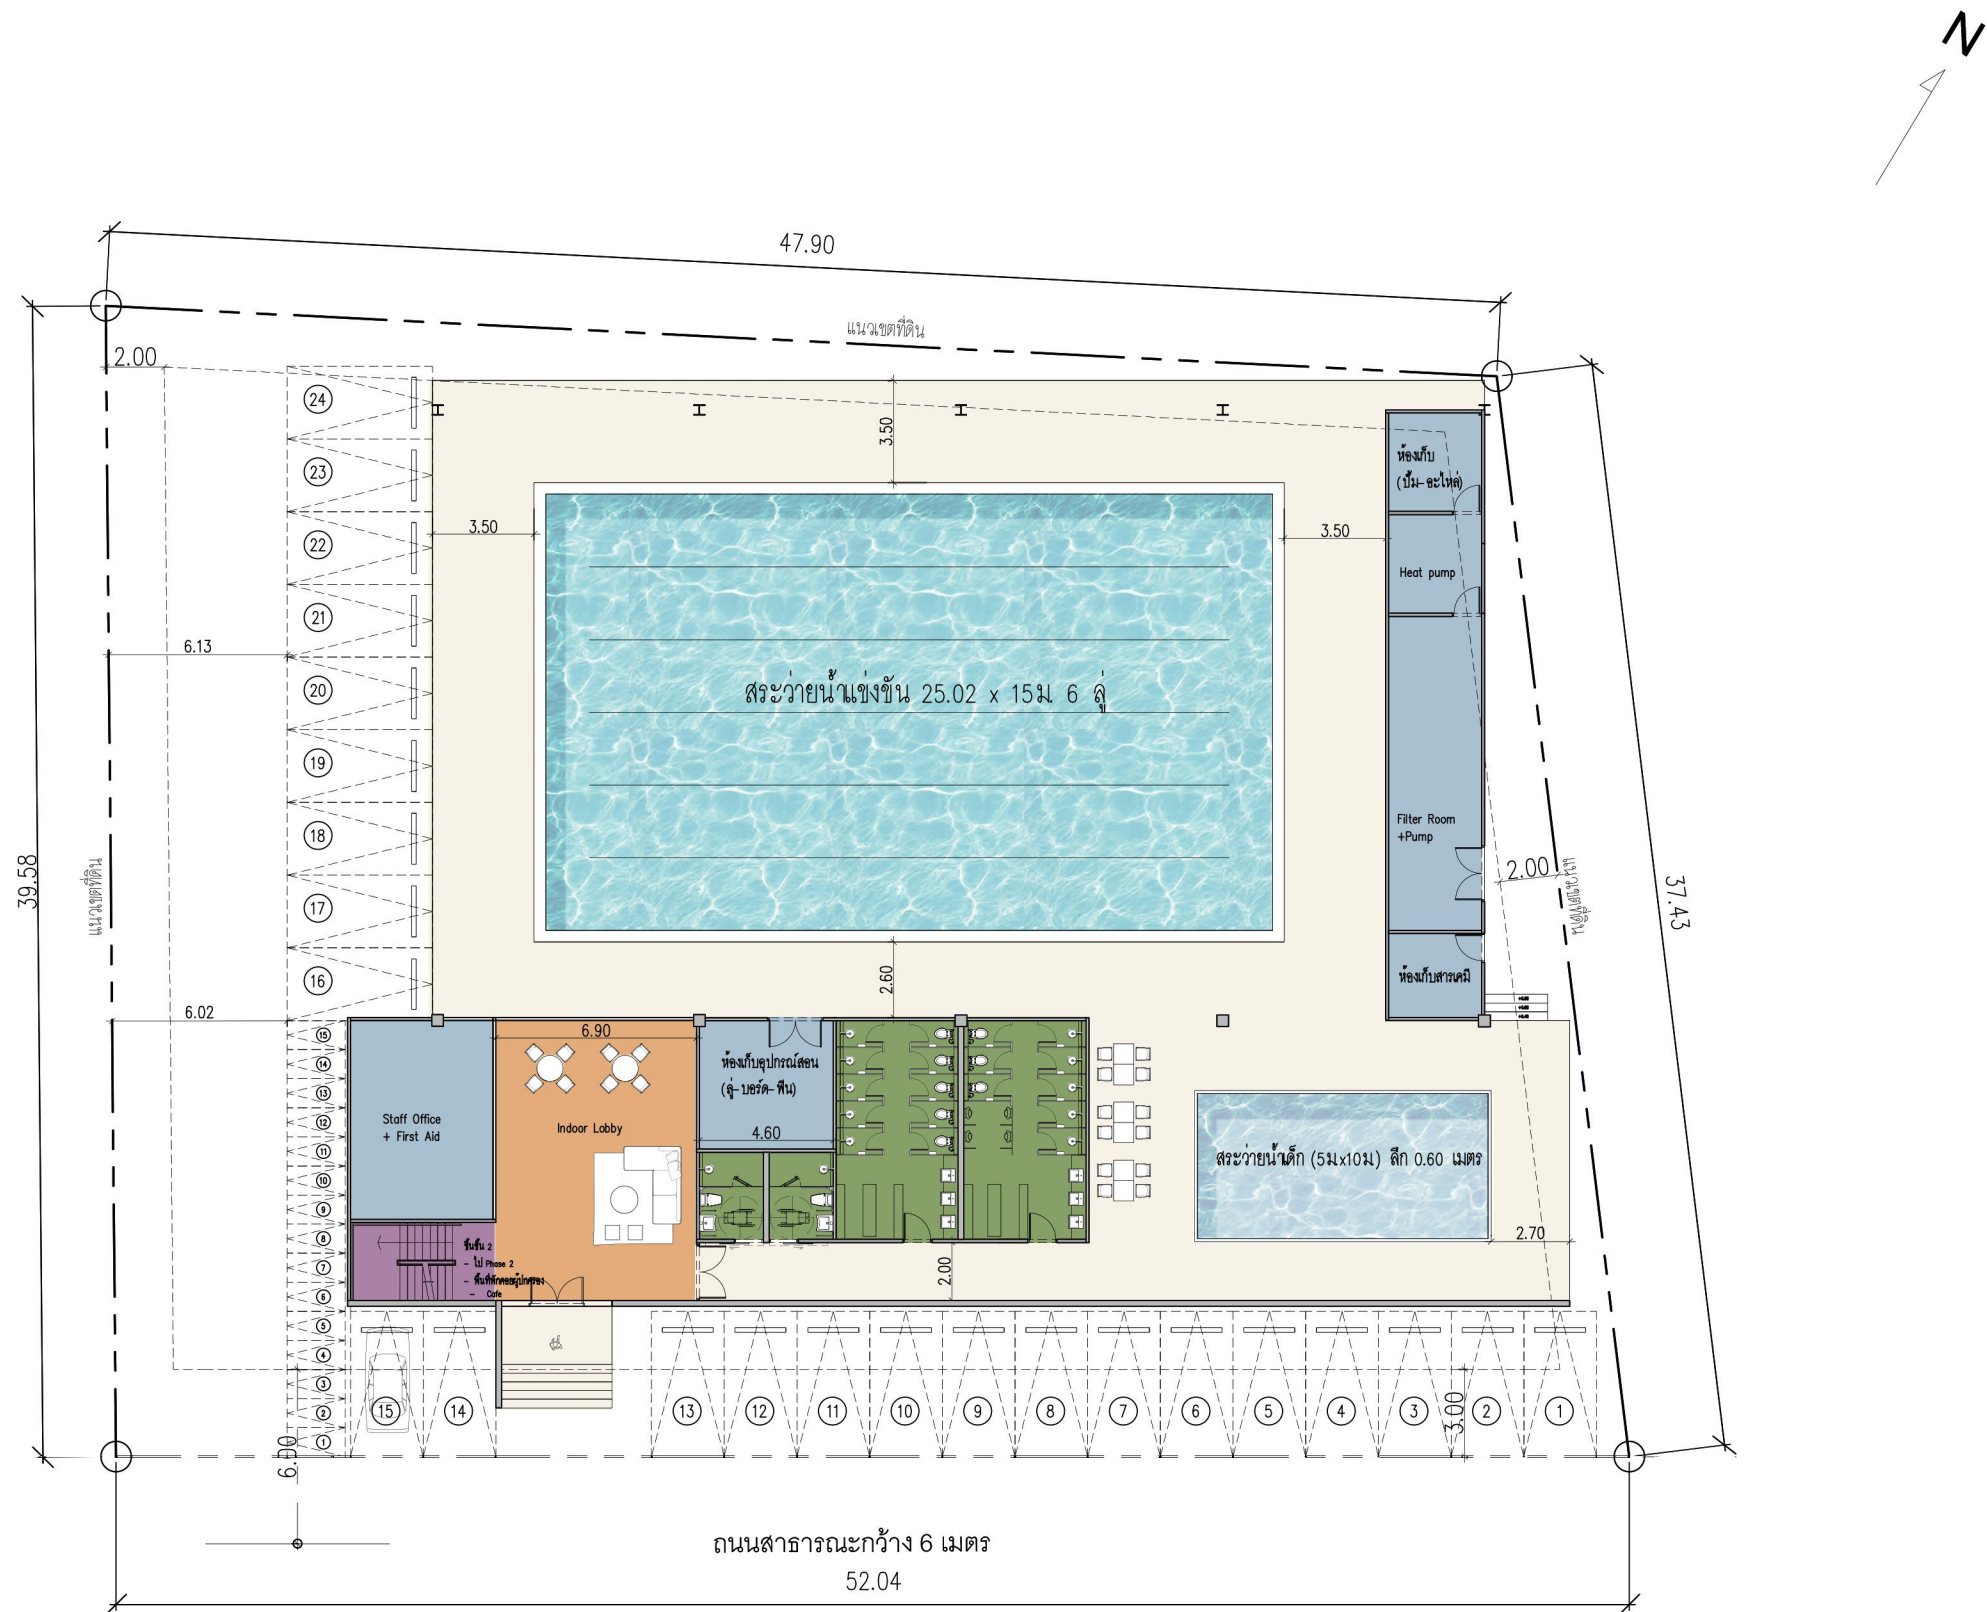

ARCHE AQUATICS

Design for Feasibility Study  
Scope M2 · 3 ทางเลือกฝั่ง · 30.08.2026

OPTION 1    ชั้น 2

คุมทางเข้าเป็นหลัก  
พัฒนาจาก OPTION 3 (Meeting 1)

|                                                                                      |             |
|--------------------------------------------------------------------------------------|-------------|
| ตัวเลขพื้นที่โดยประมาณ                                                               |             |
| พื้นที่อาคาร ชั้น 1 + ชั้น 2                                                         | 559.6 ตร.ม. |
| ดาครอบสระ + ทางสัญจร                                                                 | 487.4 ตร.ม. |
| ผิวน้ำสระ (แข่ง 375.3 + เด็ก 50.0)                                                   | 425.3 ตร.ม. |
| หลังคาคลุมสระ 36 × 21 ม.                                                             | 756.0 ตร.ม. |
| ที่จอดรถ                                                                             | 24 คัน      |
| ตัวเลขจากการวัดบนแบบ ยังไม่ได้ยืนยันใน AutoCAD ใช้เปรียบเทียบระหว่างทางเลือกเท่านั้น |             |

- สัญลักษณ์
- โซนผู้เรียน / นักกีฬา

ห้องเปลี่ยนเสื้อ อาบน้ำ ล็อกเกอร์

โซนผู้ปกครอง / สาธารณะ

ลิบบี พื้นที่พักผ่อน

Mini Café

เครื่องดื่ม ของว่าง

โซนเจ้าหน้าที่ / งานระบบ

Staff Office ห้องเครื่อง ห้องเคมี

พื้นที่ Phase 2

Fitness Dryland Multipurpose

ทางสัญจร / ดาครอบสระ

Pool deck ทางเดิน บันได

สระแข่งขัน 25 ม. 6 ลู่อ

375.3 ตร.ม.

สระเด็ก 10 × 5 ม. ลึก 0.60 ม.

50.0 ตร.ม.

ข้อดี / ข้อเสีย ของทางเลือกนี้

เทียบด้วย 4 แคนเดียวกันทุกทางเลือก

1. สายตาเจ้าหน้าที่ — จากที่นั่งประจำ มองเห็นอะไร
- + Staff Office อยู่ปลายซ้ายสุด ติดลานจอดและทางเข้า คุมคนเข้า-ออกและลานจอดได้ดีที่สุดใน 3 แบบ

- จากโต๊ะทำงาน มองไม่เห็นสระแข่งขัน

- ครูต้องออกมายืนที่ดาครอบเพื่อดูแลผู้เรียน

- มองไม่เห็นสระเด็กซึ่งอยู่คนละปลายอาคาร
2. เส้นทางเด็ก — จากระดับถึงขอบสระ ผ่านอะไรบ้าง
- + ห้องอาบน้ำและเปลี่ยนเสื้ออยู่บนแนวทางเดินไปสระพอดิ

- เด็กเปลี่ยนเสื้อเสร็จเดินตรงลงสระได้เลย ไม่ต้องย้อนทาง

- ที่จอดรถแยก 2 ฝั่ง (ด้านซ้ายและด้านหน้า)

- ยามหรือเจ้าหน้าที่ต้องเดินไปมาระหว่าง 2 จุด

- ทางเข้าอาคารติดลานจอดโดยตรง ทำเป็น drop-off ไม่ได้

- เด็กต้องเดินผ่านแนวช่องจอดรถ
3. ผู้ปกครอง — นั่งรอตรงไหน เห็นลูกหรือไม่
- + พื้นที่พักผ่อนอยู่ชั้น 2 พร้อม Mini Café มองลงมาเห็นสระจากมุมสูง

- ไม่รบกวนสมาธิผู้เรียนและผู้สอน

+ อัฒจรรย์ริมสระ รองรับได้ประมาณ 90 ที่นั่ง

- ผู้ปกครองที่ต้องดูแลเด็กเล็กใกล้ชิดต้องลงมาชั้น 1
4. การขยายในอนาคต — ต่อเติมอะไรได้โดยไม่รื้อโครงสร้าง
- + แยกห้องเก็บของออกจากห้องปั้ม

- ทำให้ขยายห้องเครื่องได้ในอนาคตโดยไม่กระทบพื้นที่อื่น

+ ชั้น 2 เตรียมโครงสร้างไว้แล้ว เปลี่ยน Multipurpose เป็น Fitness ได้ตาม Phase 2

- สระเด็กอยู่มุมขวา ไม่มีเงาอาคารบัง โดนแดดบ่ายเต็ม ต้องเผื่อบังกันแดดเพิ่ม

