


OPTION 2 ชั้น 1

คุ่มสระเป็นหลัก
พัฒนาจาก OPTION 3 (Meeting 1)

ตัวเลขพื้นที่โดยประมาณ	
พื้นที่อาคาร ชั้น 1 + ชั้น 2	568.6 ตร.ม.
คาครอบสระ + ทางสัญจร	502.6 ตร.ม.
ผิวน้ำสระ (แข่ง 375.3 + เด็ก 50.0)	425.3 ตร.ม.
หลังคาคลุมสระ 36 × 21 ม.	756.0 ตร.ม.
ที่จอดรถ	24 คัน
ตัวเลขจากการวัดบนแบบ ยังไม่ได้ยืนยันใน AutoCAD ใช้เปรียบเทียบระหว่างทางเลือกเท่านั้น	

- สัญลักษณ์สี
- โซนผู้เรียน / นักกีฬา
ห้องเปลี่ยนเสื้อ อาบน้ำ ล็อกเกอร์
 - โซนผู้ปกครอง / สาธารณะ
ลิโอบบี้ พื้นที่พักผ่อน
 - Mini Café
เครื่องดื่ม ของว่าง
 - โซนเจ้าหน้าที่ / งานระบบ
Staff Office ห้องเครื่อง ห้องเคมี
 - พื้นที่ Phase 2
Fitness Dryland Multipurpose
 - ทางสัญจร / คาครอบสระ
Pool deck ทางเดิน บันได
 - สระแข่งขัน 25 ม. 6 ลู่
375.3 ตร.ม.
 - สระเด็ก 10 × 5 ม. ลึก 0.60 ม.
50.0 ตร.ม.

- ข้อดี / ข้อเสีย ของทางเลือกนี้
- เทียบกับ 4 แคนเดียวกันทุกทางเลือก
- สายคาเจ้าหน้าที่ — จากที่นั่งประจำ มองเห็นอะไร
+ Staff Office ย้ายมาอยู่กลางอาคาร หันหน้าเข้าสู่สระแข่งขัน
 ครูเห็นทั้งเด็กที่ออกจากห้องเปลี่ยนเสื้อและคนที่อยู่ในสระจากที่นั่งเดียว
+ แก่ข้อเสียเรื่องมุมมองของ OPTION 1 โดยตรง ฝั่งส่วนอื่นเหมือนเดิมทุกอย่าง
- แลกมาด้วยการที่ทางเข้าและลานจอดไม่มีคนคุมสายตาโดยตรง
 ต้องพึ่งกล้องวงจรปิดหรือจุดยามแยก
 - เส้นทางเด็ก — จากระดับถึงขอบสระ ผ่านอะไรบ้าง
+ ห้องอาบน้ำและเปลี่ยนเสื้ออยู่บนแนวทางเดินไปสระเช่นเดียวกับ OPTION 1
+ ลิโอบบี้กว้างขึ้นเป็น 7.15 ม. รับผู้ใช้ช่วง peak 16.00–20.30 น. ได้ดีกว่า OPTION 1
- ที่จอดรถแยก 2 ฝั่ง และทางเข้าติดลานจอด ทำ drop-off ไม่ได้ เหมือน OPTION 1
 - ผู้ปกครอง — นั่งรอตรงไหน เห็นลูกหรือไม่
+ พื้นที่พักผ่อนชั้น 2 พร้อม Mini Café เหมือน OPTION 1
+ อัฒจันทร์ริมสระ รองรับได้ประมาณ 90 ที่นั่ง
- ผู้ปกครองเด็กเล็กยังต้องลงมาชั้น 1 เหมือนเดิม
 - การขายในอนาคด — ต่อเติมอะไรได้โดยไม่รื้อโครงสร้าง
+ ย้ายห้องเก็บอุปกรณ์สอนไปปลายซ้าย ทำให้แกนกลางอาคารเป็นโซนควบคุม
 ปรับ function ในอนาคดได้ง่ายกว่า
+ ห้องเครื่องขยายได้เหมือน OPTION 1
- สระเด็กยังอยู่มุมขวา ไม่มีเงาอาคารบัง เหมือน OPTION 1

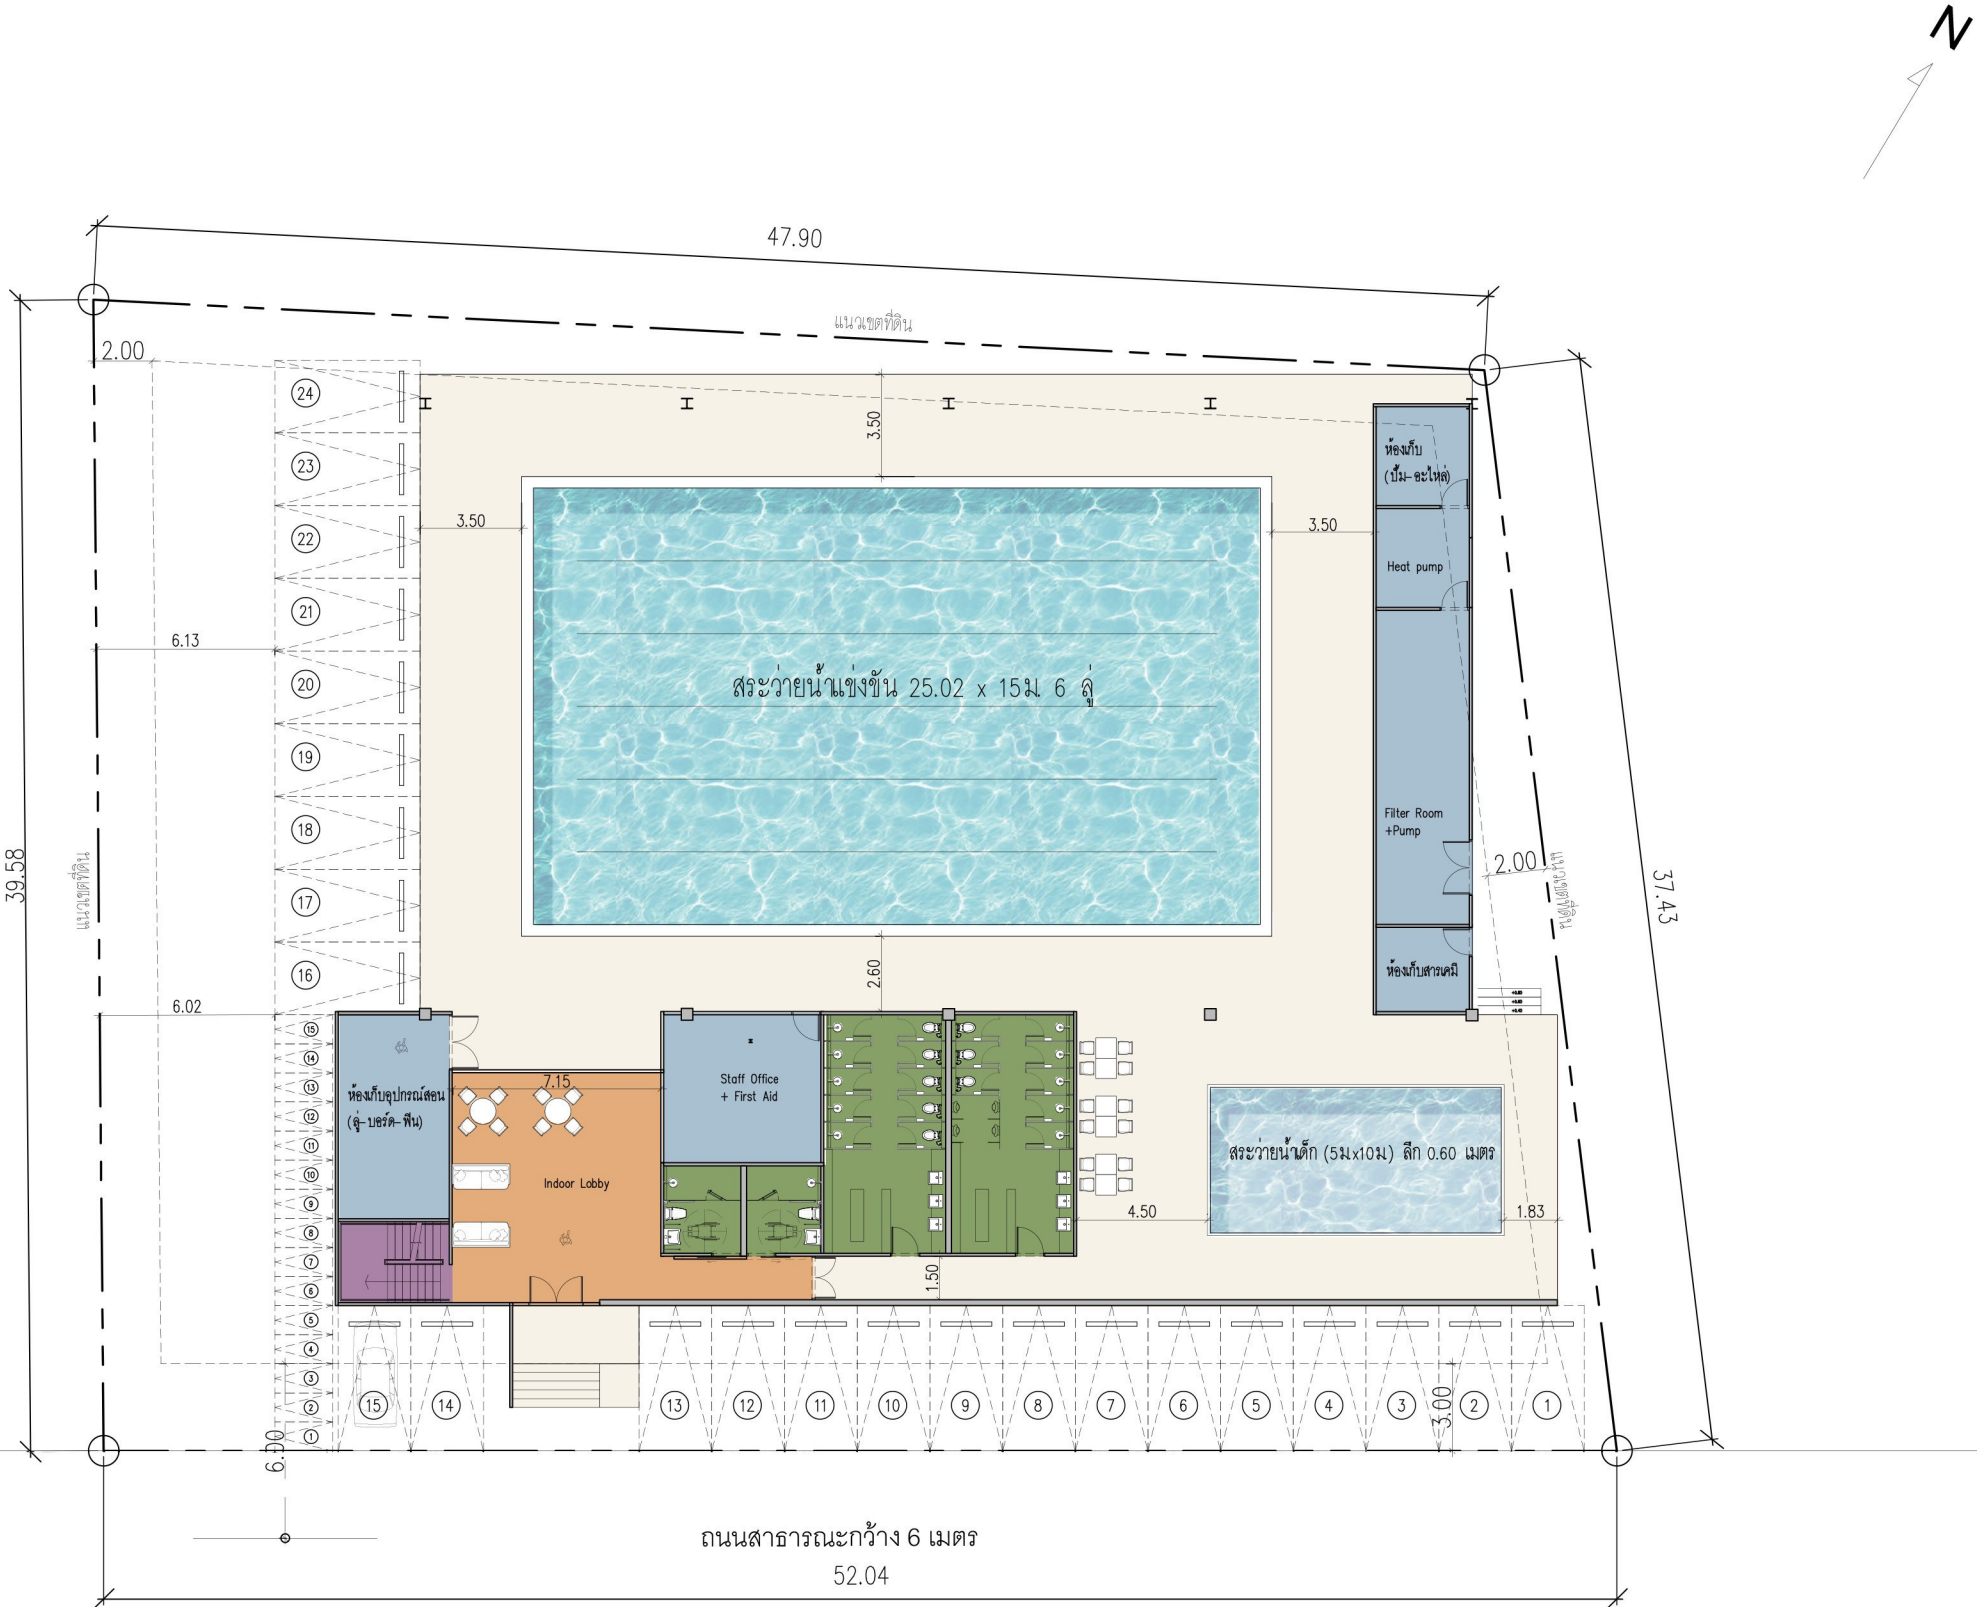

ARCHE AQUATICS

Design for Feasibility Study
Scope M2 · 3 ทางเลือกฝั่ง · 30.08.2026

OPTION 2 ชั้น 2

คุ่มสระเป็นหลัก
พัฒนาจาก OPTION 3 (Meeting 1)

ตัวเลขพื้นที่โดยประมาณ	
พื้นที่อาคาร ชั้น 1 + ชั้น 2	568.6 ตร.ม.
ดาครอบสระ + ทางสัญจร	502.6 ตร.ม.
ผิวน้ำสระ (แข่ง 375.3 + เด็ก 50.0)	425.3 ตร.ม.
หลังคาคลุมสระ 36 × 21 ม.	756.0 ตร.ม.
ที่จอดรถ	24 คัน
ตัวเลขจากการวัดบนแบบ ยังไม่ได้ยืนยันใน AutoCAD ใช้เปรียบเทียบระหว่างทางเลือกเท่านั้น	

- สัญลักษณ์สี
- โซนผู้เรียน/ นักกีฬา
ห้องเปลี่ยนเสื้อ อาบน้ำ ล็อกเกอร์
 - โซนผู้ปกครอง/ สาธารณะ
ลิโอบบี้ พื้นที่พักผ่อน
 - Mini Café
เครื่องดื่ม ของว่าง
 - โซนเจ้าหน้าที่/ งานระบบ
Staff Office ห้องเครื่อง ห้องเคมี
 - พื้นที่ Phase 2
Fitness Dryland Multipurpose
 - ทางสัญจร/ ดาครอบสระ
Pool deck ทางเดิน บันได
 - สระแข่งขัน 25 ม. 6 ลู่
375.3 ตร.ม.
 - สระเด็ก 10 × 5 ม. ลึก 0.60 ม.
50.0 ตร.ม.

- ข้อดี / ข้อเสีย ของทางเลือกนี้
- เทียบกับ 4 แคนเดียวกันทุกทางเลือก
- สายคาเจ้าหน้าที่ — จากที่นั่งประจำ มองเห็นอะไร
 - + Staff Office ย้ายมาอยู่กลางอาคาร หันหน้าเข้าสู่สระแข่งขัน
ครูเห็นทั้งเด็กที่ออกจากห้องเปลี่ยนเสื้อและคนที่อยู่ในสระจากที่นั่งเดียว
 - + แก้ข้อเสียเรื่องมุมมองของ OPTION 1 โดยตรง ฝั่งส่วนอื่นเหมือนเดิมทุกอย่าง
 - แลกมาด้วยการที่ทางเข้าและลานจอดไม่มีคนคุมสายตาโดยตรง
ต้องพึ่งกล้องวงจรปิดหรือจุดยามแยก
 - เส้นทางเด็ก — จากระดับถึงขอบสระ ผ่านอะไรบ้าง
 - + ห้องอาบน้ำและเปลี่ยนเสื้ออยู่บนแนวทางเดินไปสระเช่นเดียวกับ OPTION 1
 - + ลิโอบบี้กว้างขึ้นเป็น 7.15 ม. รับผู้ใช้ช่วง peak 16.00–20.30 น. ได้ดีกว่า OPTION 1
 - ที่จอดรถแยก 2 ฝั่ง และทางเข้าติดลานจอด ทำ drop-off ไม่ได้ เหมือน OPTION 1
 - ผู้ปกครอง — นั่งรอตรงไหน เห็นลูกหรือไม่
 - + พื้นที่พักผ่อนชั้น 2 พร้อม Mini Café เหมือน OPTION 1
 - + อัฒจันทร์ริมสระ รองรับได้ประมาณ 90 ที่นั่ง
 - ผู้ปกครองเด็กเล็กยังต้องลงมาชั้น 1 เหมือนเดิม
 - การขายในอนาคต — ต่อเติมอะไรได้โดยไม่รื้อโครงสร้าง
 - + ย้ายห้องเก็บอุปกรณ์สอนไปปลายซ้าย ทำให้แกนกลางอาคารเป็นโซนควบคุม
ปรับ function ในอนาคตได้ง่ายกว่า
 - + ห้องเครื่องขยายได้เหมือน OPTION 1
 - สระเด็กยังอยู่มุมขวา ไม่มีเงาอาคารบัง เหมือน OPTION 1

