

Design for Feasibility Study  
Scope M2 · 3 ทางเลือกผัง · 30.08.2026

พัฒนจาก OPTION 4 (Meeting 1)


|                                    |             |
|------------------------------------|-------------|
| ตัวเลขพื้นที่โดยประมาณ             |             |
| พื้นที่อาคาร ชั้น 1 + ชั้น 2       | 538.7 ตร.ม. |
| คาบรอบสระ + ทางสัญจร               | 532.7 ตร.ม. |
| ผิวน้ำสระ (แข่ง 375.3 + เด็ก 50.0) | 425.3 ตร.ม. |
| หลังคาคลุมสระ 36 × 21 ม.           | 756.0 ตร.ม. |
| ทั้งหมด                            | 24 คน       |

ตัวเลขจากการคำนวณแบบ ยังไม่ได้ยืนยันใน AutoCAD ขึ้นเปรียบเทียบระหว่างทางเลือกเท่านั้น

-  **โซนผู้เรียน / นักกีฬา**  
ห้องเปลี่ยนเสื้อ อาบน้ำ ลีกกเกอร์
-  **โซนผู้ปกครอง / สาธารณะ**  
ล็อบบี้ พื้นที่พักผ่อน
-  **Mini Café**  
เครื่องดื่ม เครื่องว่าง
-  **โซนเจ้าหน้าที่ / งานระบบ**  
Staff Office ห้องเครื่อง ห้องเคมี
-  **พื้นที่ Phase 2**  
Fitness Dryland Multipurpose
-  **ทางสัญจร / คาคอบบอส**  
Pool deck ทางเดิน บันได
-  **สระน้ำแข่งขัน 25 ม. 6 ลู**  
375.3 ตร.ม.
-  **สระเด็ก 10 x 5 ม. ลึก 0.60 ม.**  
50.0 ตร.ม.

เทียบกับ 4 แกนเดียวกันทุกทางเลือก

1. **สายคาเจ้าหน้าที – จากที่นั่งประจำ มองเห็นอะไร**
  - + Staff Office เห็นทั้งสระแข่งขันและสระเด็กพร้อมกันจากจุดเดียวครอบคลุมที่สุดใน 3 แบบ
  - + สระทั้งสองอยู่ในโซนสายคาเดียวกัน ลดจำนวนเจ้าหน้าที่ที่ต้องประจำจุด
  - ห้อง Staff Office เล็กกว่า OPTION 1 และ 2 ต้องตรวจสอบว่าพอสำหรับทีมงาน 4-5 คนพร้อมที่เก็บเอกสาร
2. **เส้นทางเด็ก – จากระถถึงขอบสระ ผ่านอะไรบ้าง**
  - + ที่จอดรถรวมเป็นแถบเดียวด้านหน้า เดินรถ one-way ได้จริง คมจุดเดียว
  - + มีพื้นที่ drop-off จัดเตรียมต่อเนื่องหลายคัน
  - + เด็กเดินเข้าอาคารได้โดยไม่ต้องคิดผ่านแนวช่องจอด
  - ตรงกึ่งกลางกับวงล้อหลักของเจ้าของโครงการ
  - ทางเข้าห้องน้ำเชื่อมทับกับพื้นที่สระเด็ก
  - คนเดินไปห้องน้ำกับเด็กที่กำลังเรียนใช้ทางเดียวกัน ต้องแก้ไขชั้น Design Development
3. **ผู้ปกครอง – นั่งรอตรงไหน เห็นลูกหรือไม่**
  - + อัดจรรย์ 4 ชั้น รองรับได้ประมาณ 120 ที่นั่ง มากที่สุดใน 3 แบบ
  - + ชั้น 2 เป็นแถบยาวขนานสระ มองเห็นสระจากด้านข้างตลอดแนว
  - + วันแข่งขัน เปลี่ยนพื้นที่ Indoor Dryland เป็นพื้นที่ชมการแข่งขันเพิ่มเติม
4. **การขยายในอนาคต – ต่อเติมอะไรได้โดยไม่มีข้อโครงสร้าง**
  - + พื้นที่ห้องเครื่องและงานระบบสระใหญ่ที่สุด
  - + รองรับการเพิ่มอุปกรณ์และการซ่อมบำรุงระยะยาวได้ดีที่สุด
  - + สระเด็กอยู่ใต้ร่มเงาอาคาร ลดแดดบายน ไม่ต้องลงทุนกันแดดเพิ่ม
  - + ชั้น 2 มีพื้นที่โล่งมาก ก็นำห้องเพิ่มได้ภายหลังเมื่อรู้ความต้องการจริง
  - โดยไม่ต้องรอโครงสร้างเพิ่ม

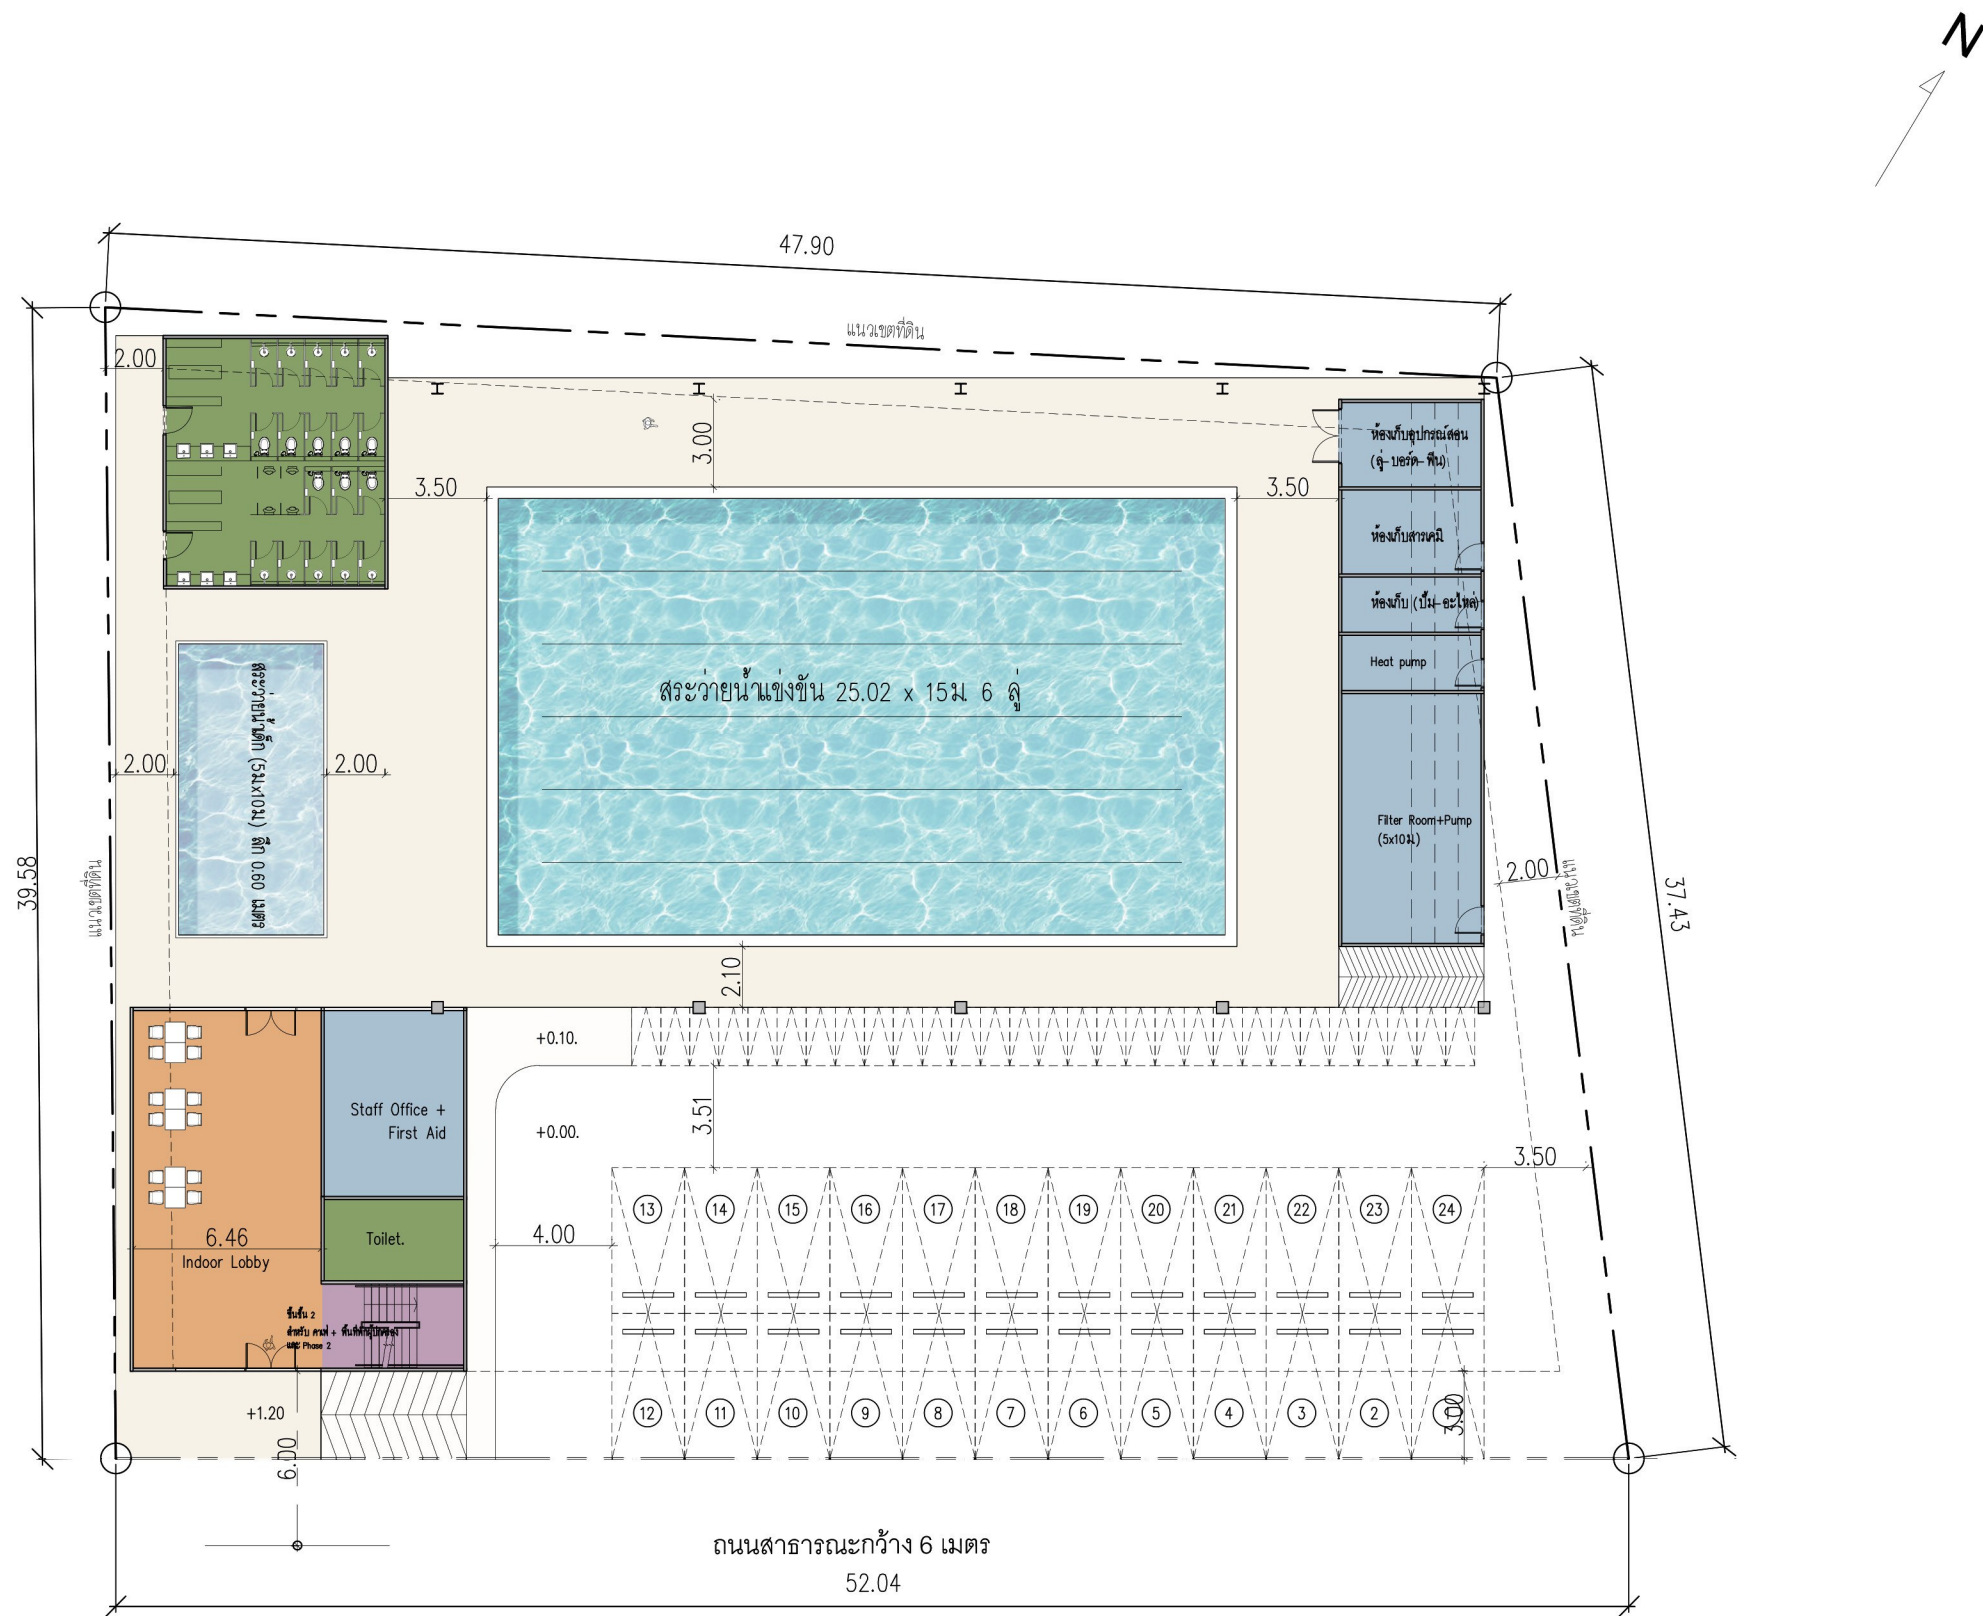

ARCHE AQUATICS

Design for Feasibility Study  
Scope M2 · 3 ทางเลือกฝั่ง · 30.08.2026

OPTION 3 <sup>ชั้น 2</sup>

คุ่มทั้งสองสระ + one-way  
พัฒนาจาก OPTION 4 (Meeting 1)

|                                                                                      |             |
|--------------------------------------------------------------------------------------|-------------|
| ตัวเลขพื้นที่โดยประมาณ                                                               |             |
| พื้นที่อาคาร ชั้น 1 + ชั้น 2                                                         | 538.7 ตร.ม. |
| ดาครอบสระ + ทางสัญจร                                                                 | 532.7 ตร.ม. |
| ผิวน้ำสระ (แข่ง 375.3 + เด็ก 50.0)                                                   | 425.3 ตร.ม. |
| หลังคาคลุมสระ 36 × 21 ม.                                                             | 756.0 ตร.ม. |
| ที่จอดรถ                                                                             | 24 คัน      |
| ตัวเลขจากการวัดบนแบบ ยังไม่ได้ยืนยันใน AutoCAD ใช้เปรียบเทียบระหว่างทางเลือกเท่านั้น |             |

- สัญลักษณ์สี
- โซนผู้เรียน / นักกีฬา  
ห้องเปลี่ยนเสื้อ อาบน้ำ ล็อกเกอร์
  - โซนผู้ปกครอง / สาธารณะ  
ลิโอบบี้ พื้นที่พักผ่อน
  - Mini Café  
เครื่องดื่ม ของว่าง
  - โซนเจ้าหน้าที่ / งานระบบ  
Staff Office ห้องเครื่อง ห้องเคมี
  - พื้นที่ Phase 2  
Fitness Dryland Multipurpose
  - ทางสัญจร / ดาครอบสระ  
Pool deck ทางเดิน บันได
  - สระแข่งขัน 25 ม. 6 ลู่วิ่ง  
375.3 ตร.ม.
  - สระเด็ก 10 × 5 ม. ลึก 0.60 ม.  
50.0 ตร.ม.

- ข้อดี / ข้อเสีย ของทางเลือกนี้
- เทียบกับ 4 แคนเดียวกันทุกทางเลือก
- สายตาเจ้าหน้าที่ — จากที่นั่งประจำ มองเห็นอะไร  
+ Staff Office เห็นทั้งสระแข่งขันและสระเด็กพร้อมกันจากจุดเดียว ครอบคลุมที่สุดใน 3 แบบ  
+ สระทั้งสองอยู่ในโซนสายตาเดียวกัน ลดจำนวนเจ้าหน้าที่ที่ต้องประจำจุด  
- ห้อง Staff Office เล็กกว่า OPTION 1 และ 2 ต้องตรวจสอบว่าพอสำหรับทีมงาน 4-5 คนพร้อมที่เก็บเอกสาร
  - เส้นทางเด็ก — จากระดับถึงขอบสระ ผ่านอะไรบ้าง  
+ ที่จอดรถรวมเป็นแถบเดียวด้านหน้า เดินรถ one-way ได้จริง คุ่มจุดเดียว  
+ มีพื้นที่ drop-off จอดเทียบต่อเนื่องหลายคัน  
เด็กเดินเข้าอาคารได้โดยไม่ต้องตัดผ่านแนวช่องจอด ตรงกับความกังวลหลักของเจ้าของโครงการ  
- ทางเข้าห้องน้ำเชื่อมทับกับพื้นที่สระเด็ก คนเดินไปห้องน้ำกับเด็กที่กำลังเรียนใช้ทางเดียวกัน ต้องแก้ไขในขั้น Design Development
  - ผู้ปกครอง — นั่งรอตรงไหน เห็นลูกหรือไม่  
+ อัฒจรรย์ 4 ชั้น รองรับได้ประมาณ 120 ที่นั่ง มากที่สุดใน 3 แบบ  
+ ชั้น 2 เป็นแถวยาวขนานสระ มองเห็นสระจากด้านข้างตลอดแนว  
+ วันแข่งขัน เปลี่ยนพื้นที่ Indoor Dryland เป็นพื้นที่ชมการแข่งขันเพิ่มเติม
  - การขายยาในอนาคต — ต่อเติมอะไรได้โดยไม่รื้อโครงสร้าง  
+ พื้นที่ห้องเครื่องและงานระบบสระใหญ่ที่สุด  
รองรับการเพิ่มอุปกรณ์และการซ่อมบำรุงระยะยาวได้ดีที่สุด  
+ สระเด็กอยู่ใต้ร่มเงาอาคาร ลดแดดบ่าย ไม่ต้องลงทุนกันแดดเพิ่ม  
+ ชั้น 2 มีพื้นที่โล่งมาก กันห้องเพิ่มได้ภายหลังเมื่อรู้ความต้องการจริง โดยไม่ต้องรื้อโครงสร้างหลัก

